

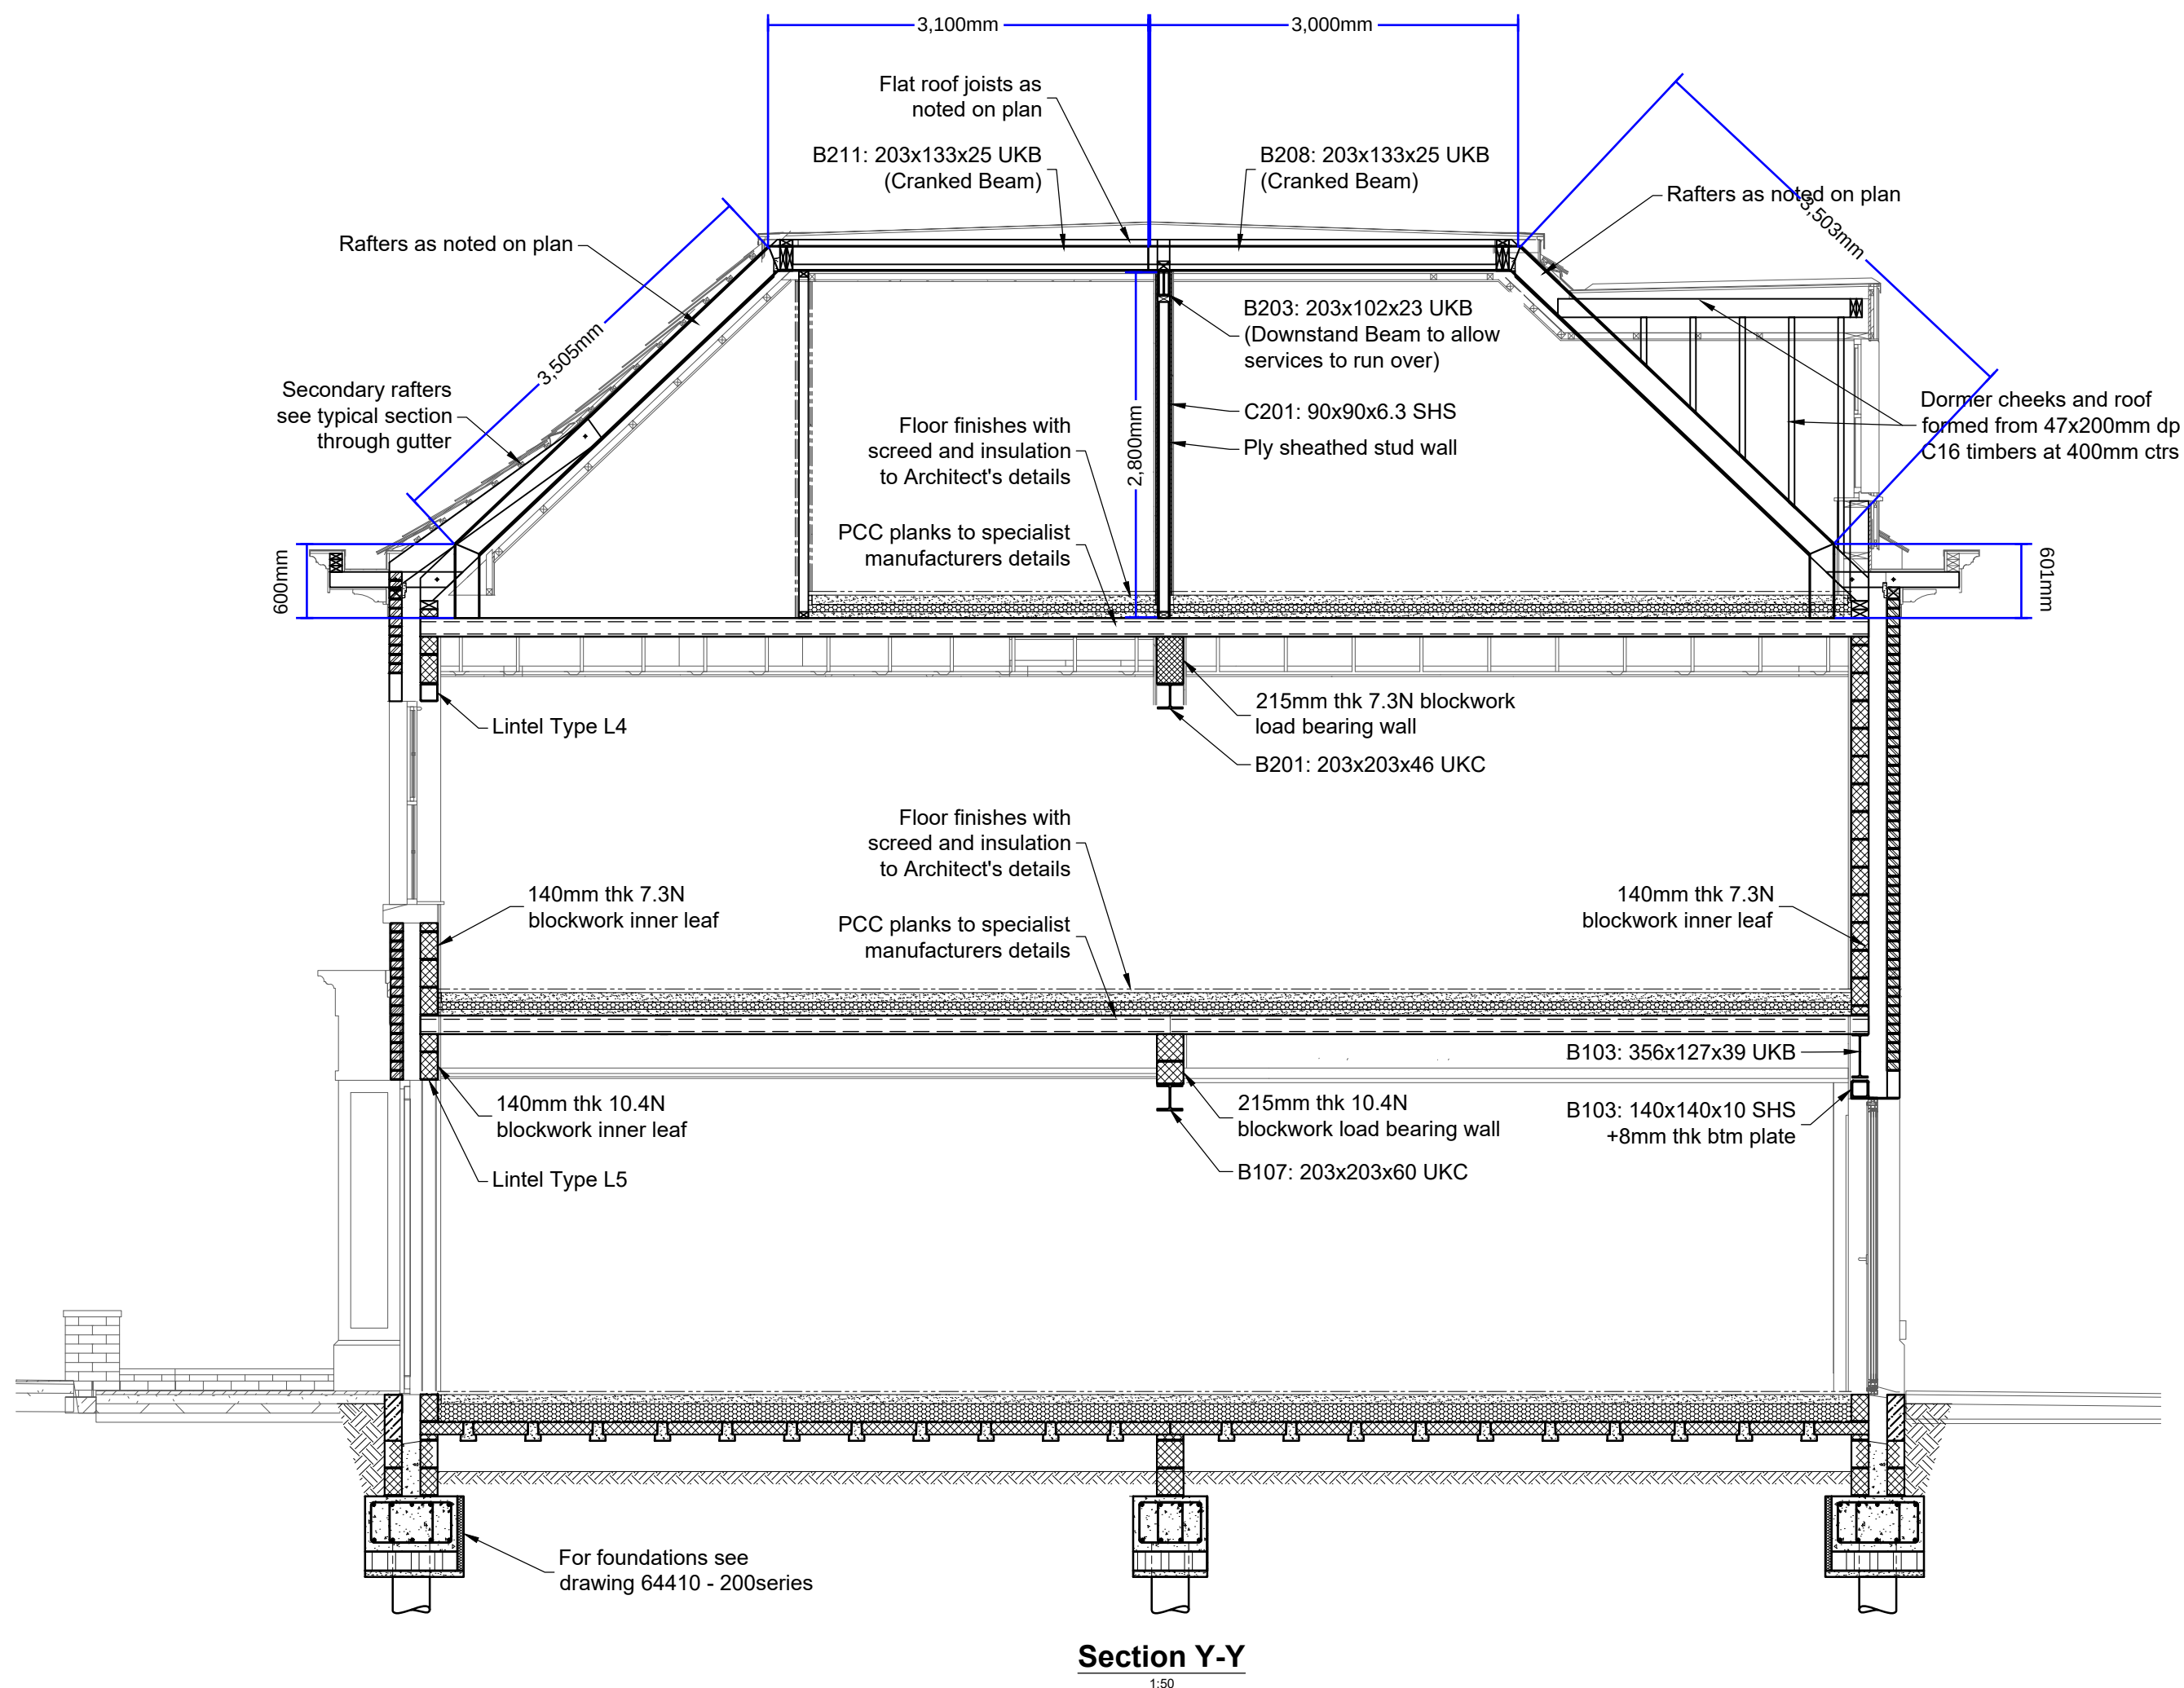


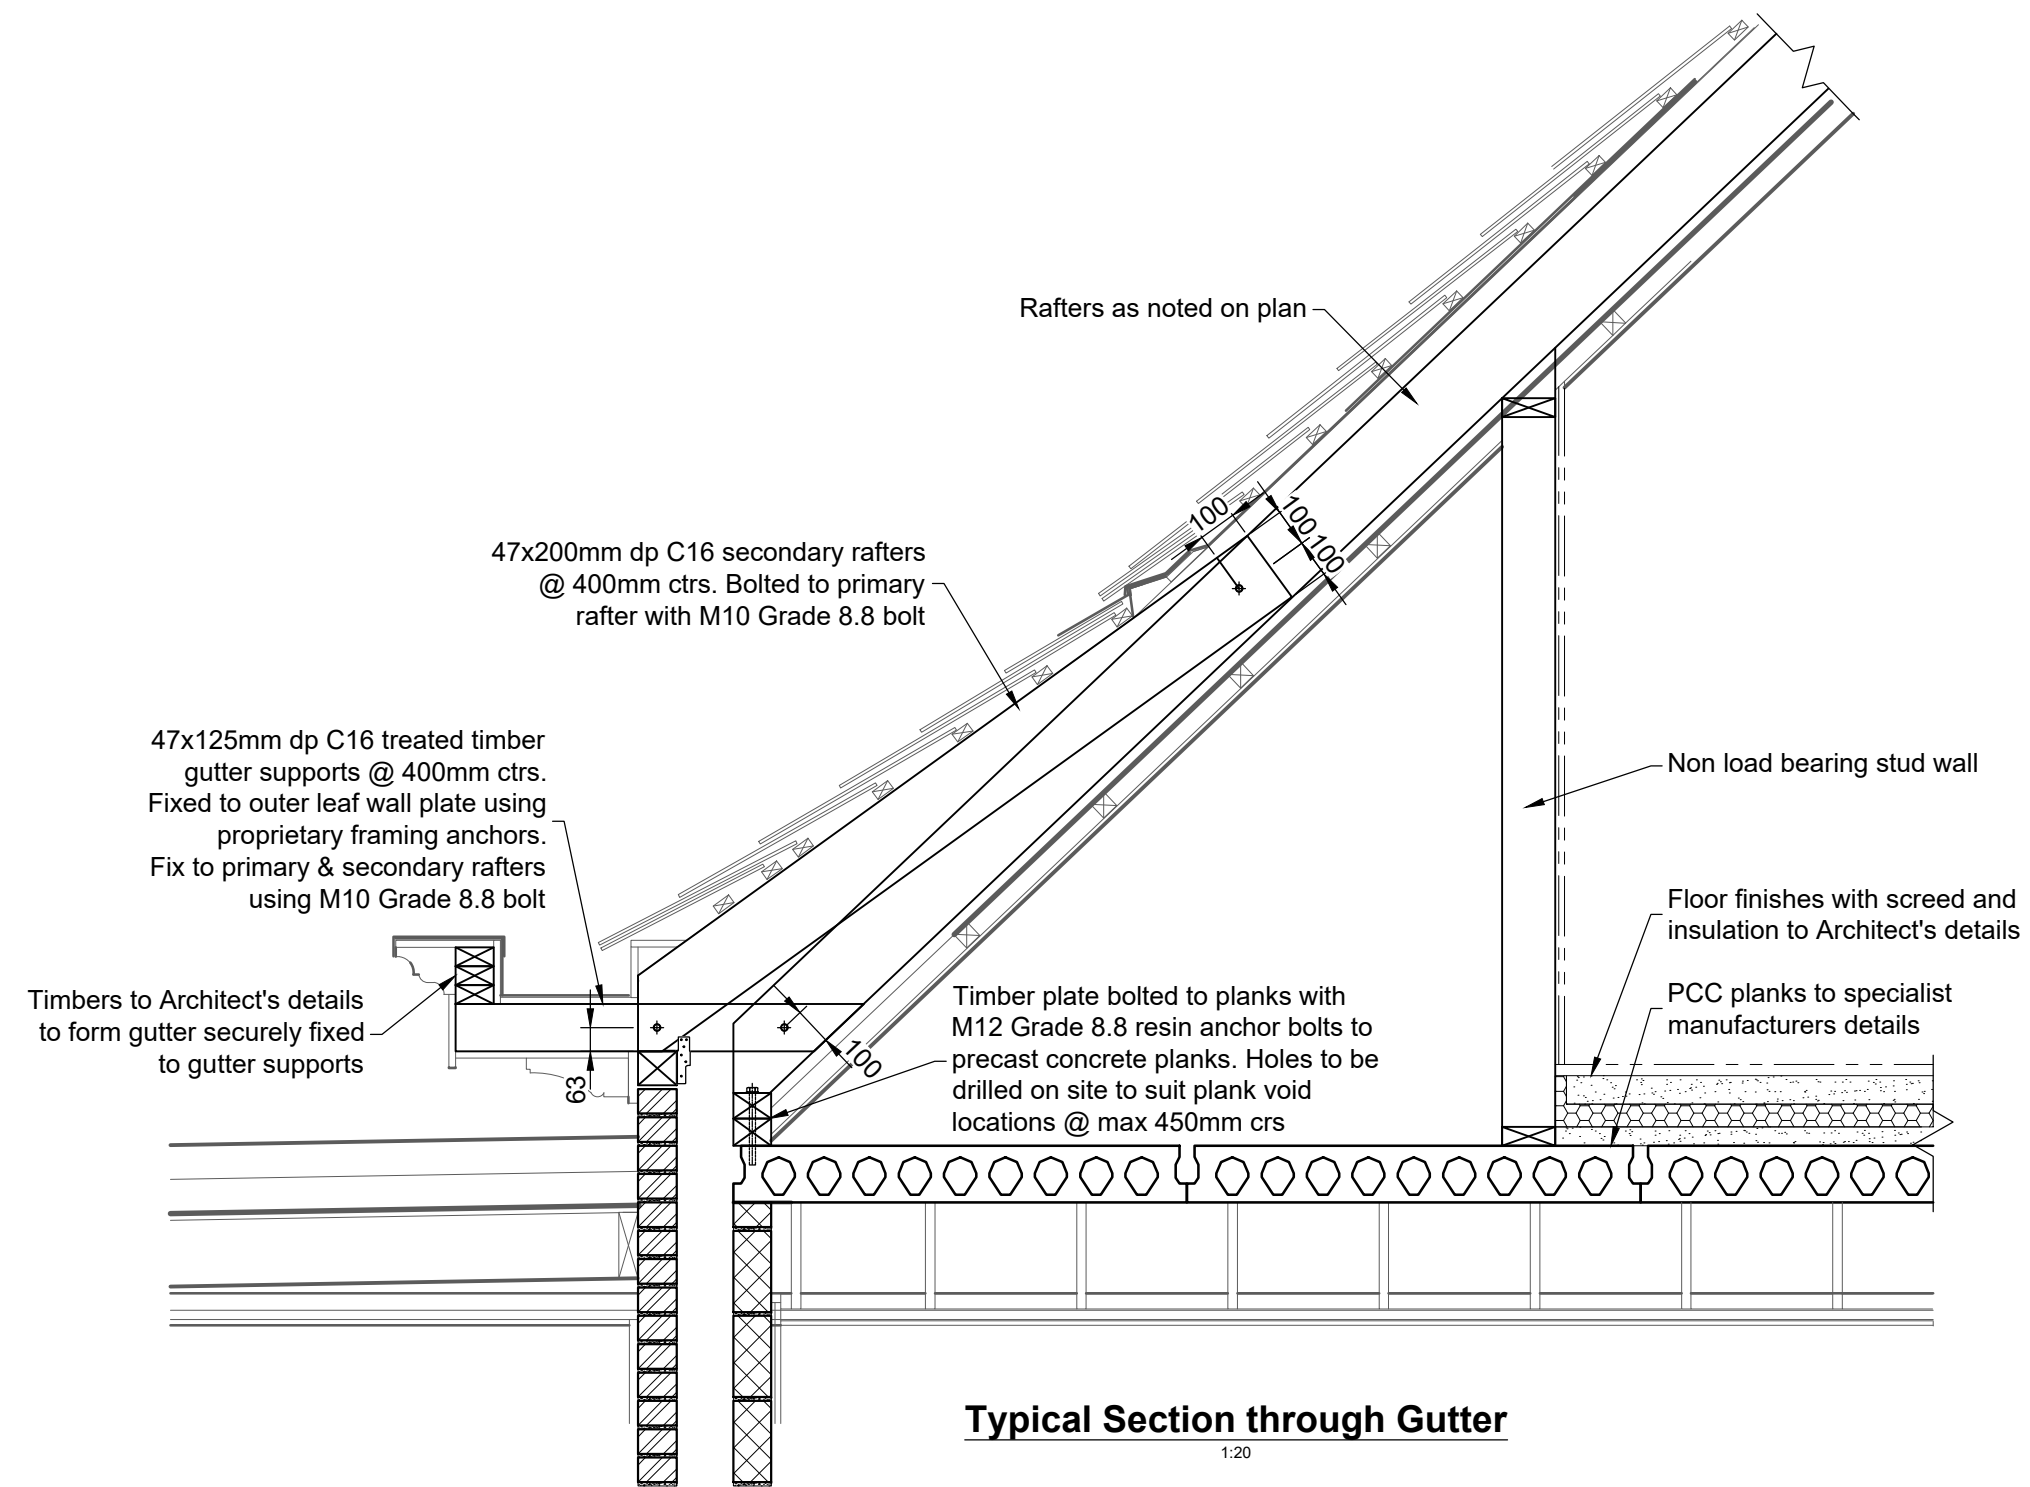

- Notes:**
- PRP have assumed the role of a Designer in the context of the Construction (Design and Management) Regulations and The Building Safety Act. All parties must be aware of their duties under this legislation.
 - Construction work shall not be started until designs have been approved by Building Control.
 - Do not scale from this drawing.
 - All dimensions are in millimetres unless noted otherwise. All levels in metres unless noted otherwise.
 - Drawing shall be read in conjunction with all relevant architect's drawings. The architect shall retain overall responsibility for dimensional control. Any inconsistencies shall be reported to PRP.
 - All levels and dimensions shall be checked on site before any work commences. Setting out remains the responsibility of others.
 - Buildings shall be constructed in accordance with Approved Document A of The Building Regulations. Drainage shall be constructed in accordance with Approved Document H of The Building Regulations.
 - Temporary works shall be designed by others to BS 5975
 - Fire protective measures shall be designed by the Architect or contractor in accordance with Approved Document B of the Building Regulations.
 - Waterproofing shall be designed by others in accordance with Approved Document C of the Building Regulations.
 - For more information see PRP drawings:
 - 64410 - 100series - Drainage and External Works
 - 64410 - 200series - Foundations
 - 64410 - 300series - Superstructure
 - This drawing must be read together with PRP drawings: 64410 - 300 - Typical Notes and Details

T2	21/11/2025	Issued for Tender	JD / HP
T1	14/11/2025	Amended to Arch comments Issued for Draft Tender	JD / HP
P2	04/11/2025	Amended to Architects comments	JD / HP
P1	15/10/2025	DRAFT Issued for comments	JD / HP
Rev	Date	Description	By / Chk

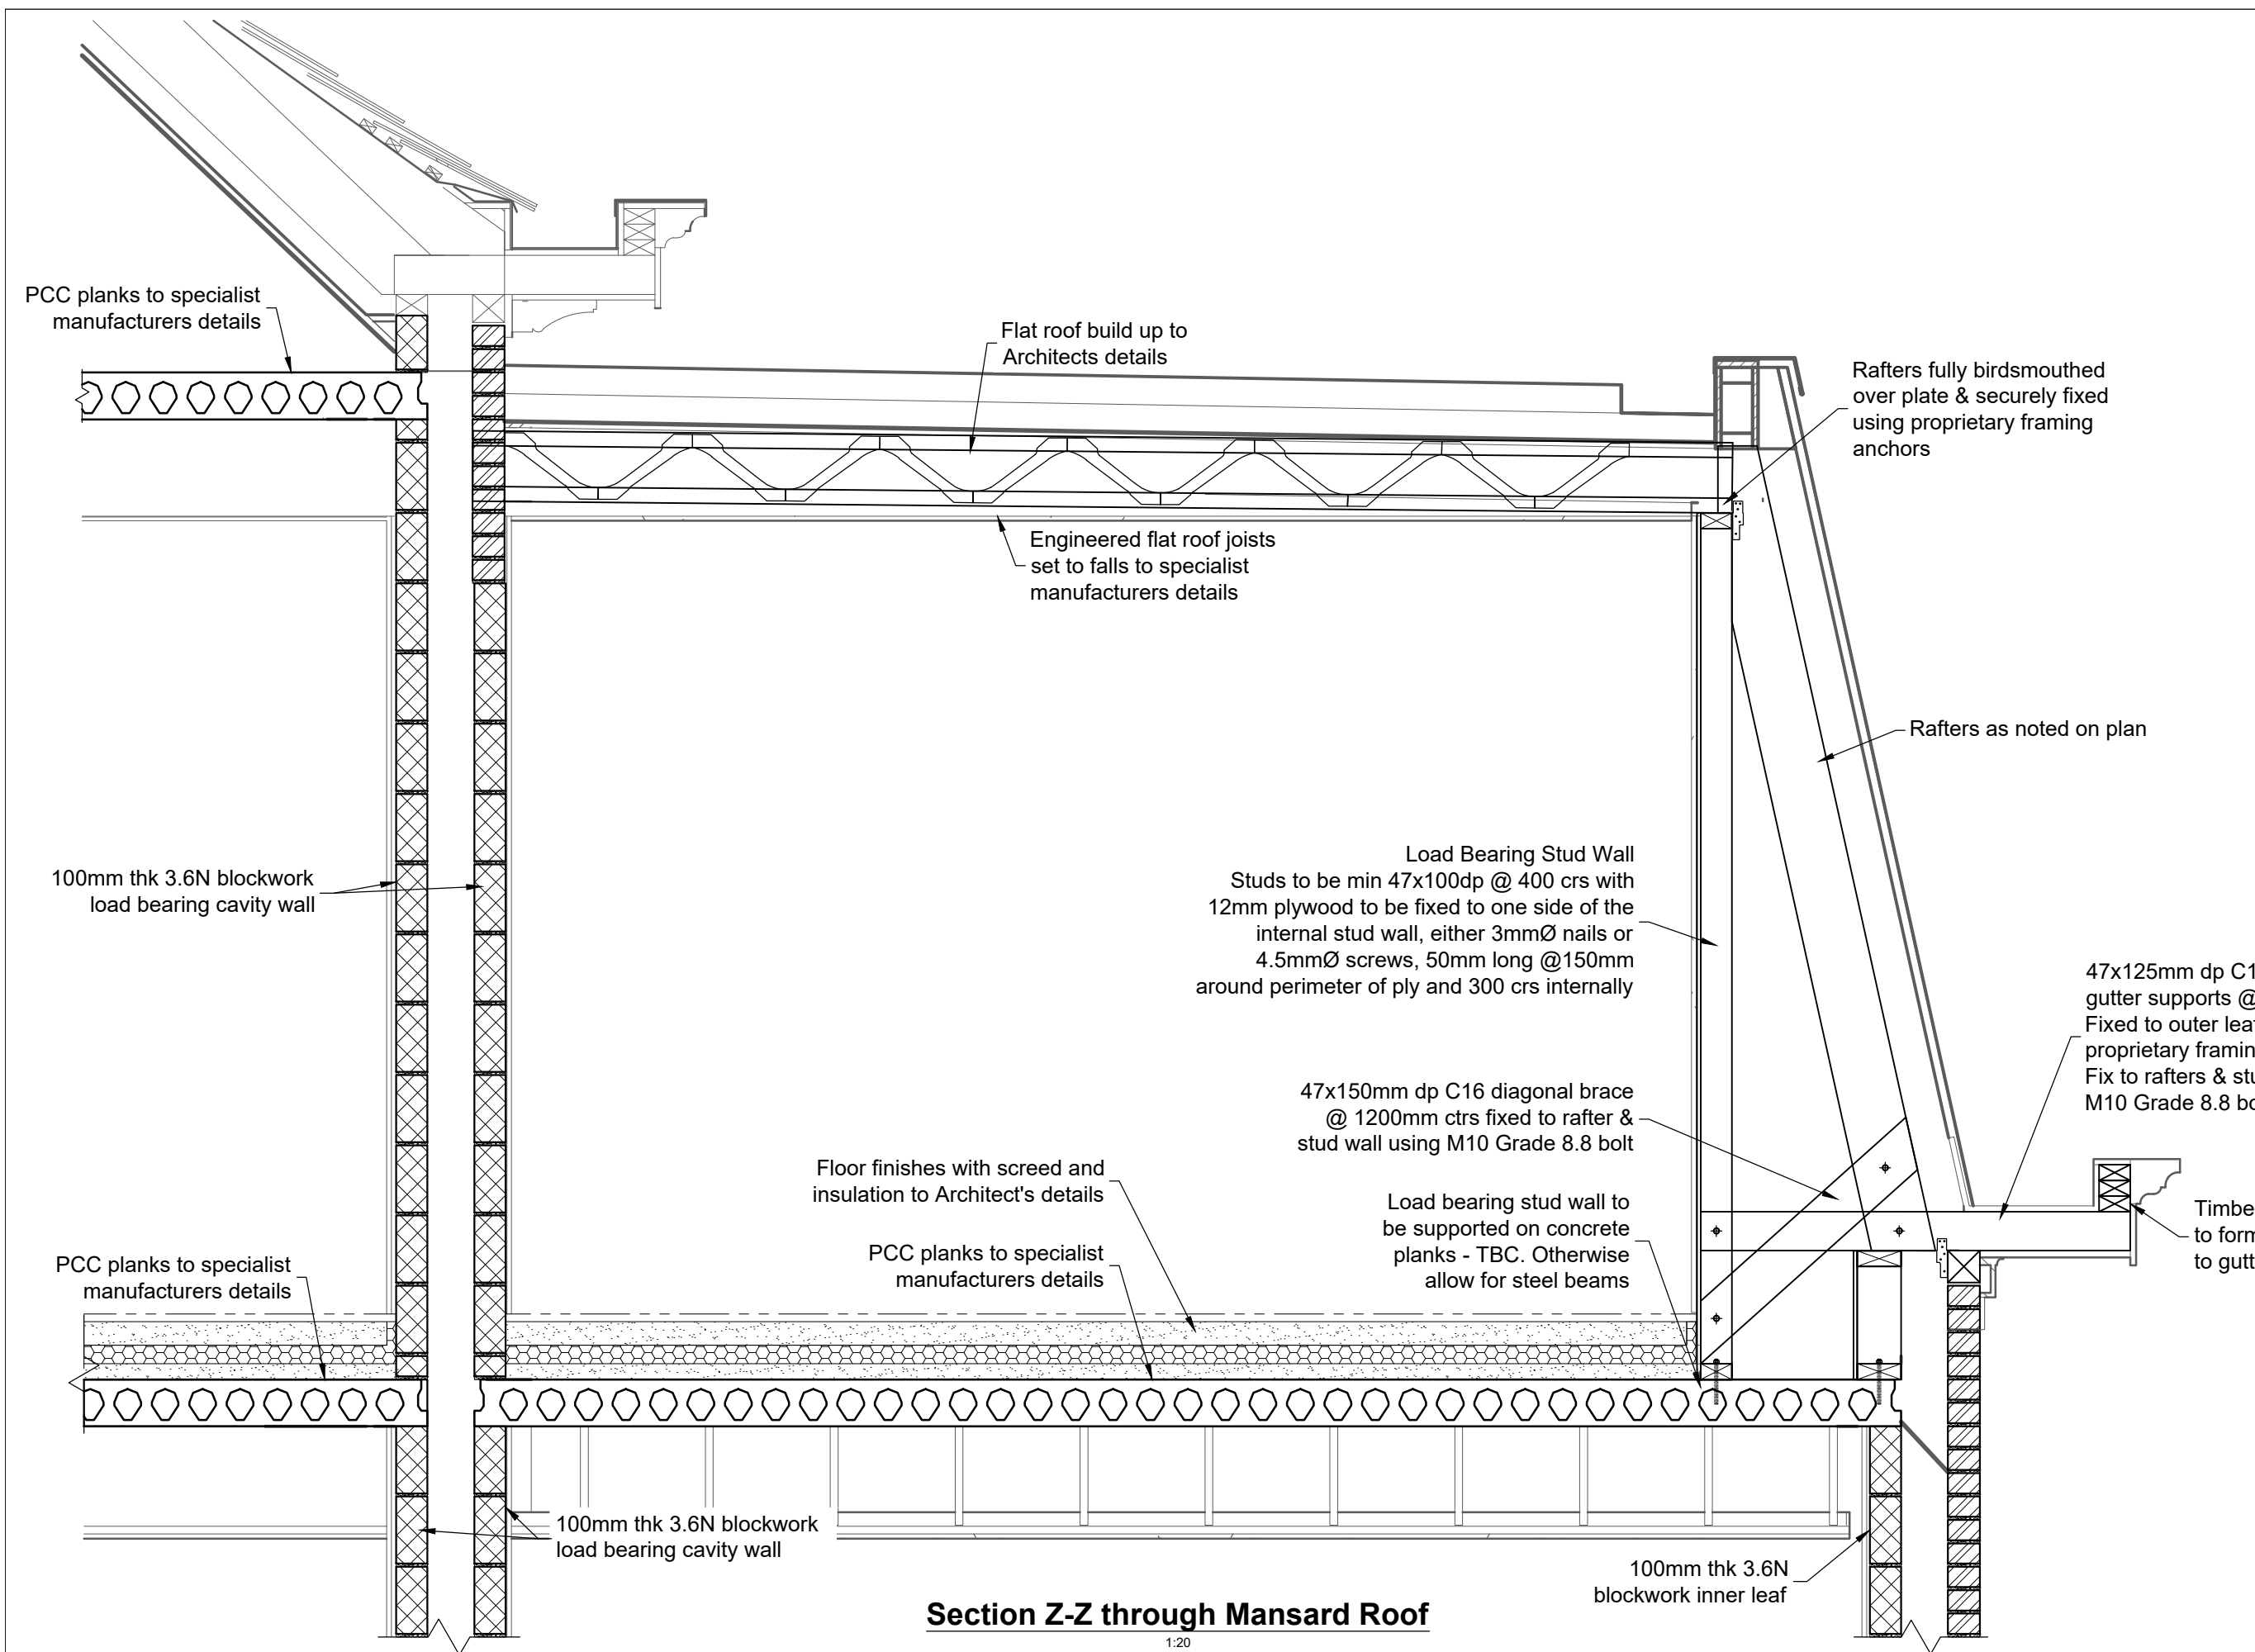

PRP
consulting engineers & surveyors

Spring Hill Office Park
Harborough Road
Pitsford NN6 9AA

Telephone: 01504 889 870
northampton@prp.uk.com
www.prp.uk.com

Leicester
Northampton
London

engineering excellence | creating advantage

Client:
St Helens Pharmacy Ltd

Architect:
Ascot Design

Project:
**33 Prestbury Road
Wilmslow
SK9 2LJ**

Title:
**Superstructure
Main House
Sections**

Status:
TENDER

Engineer:	JKT	Date:	September 2025
Drawn:	JD	Scales @ A1:	
Checked:	HP	1:50 1:20	
Project No:	64410	Drg No:	304
		Rev:	T2