


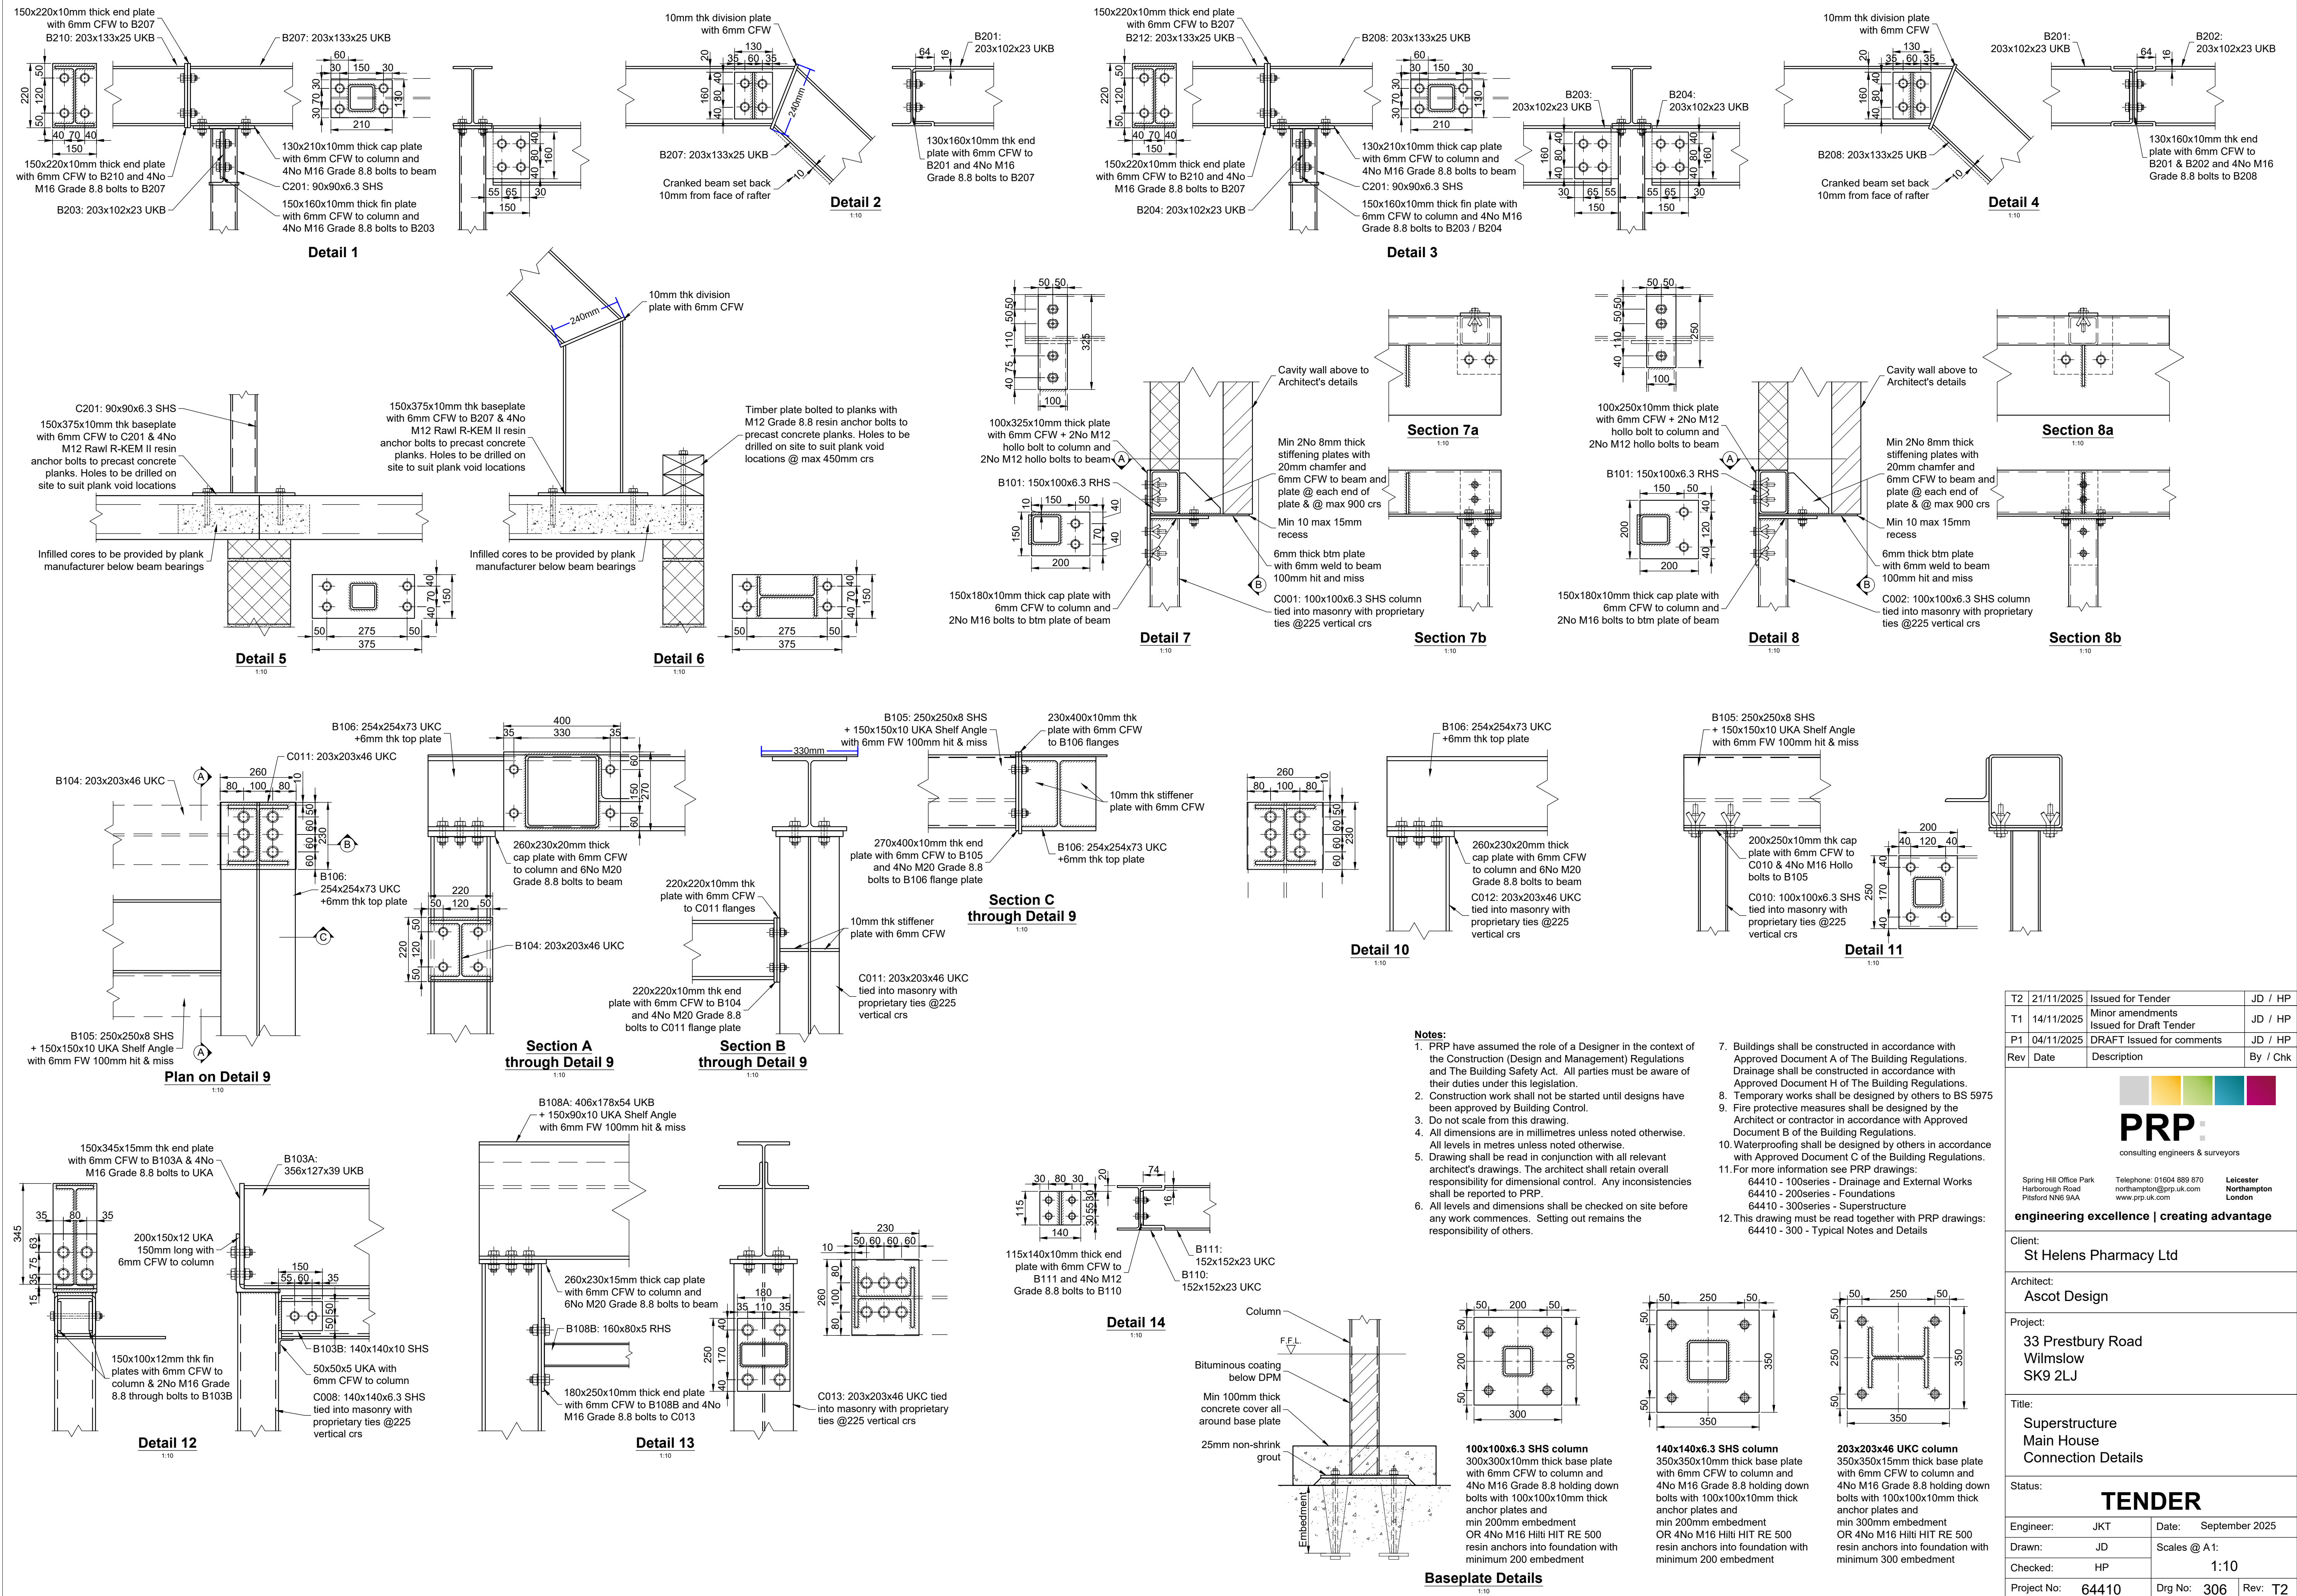

T2	21/11/2025	Issued for Tender	JD / HP
T1	14/11/2025	Minor amendments Issued for Draft Tender	JD / HP
P1	04/11/2025	DRAFT Issued for comments	JD / HP
Rev	Date	Description	By / Chk



Spring Hill Office Park
Harborough Road
Pitsoford NN6 9AA

Telephone: 01604 889 870
northampton@prp.uk.com
www.prp.uk.com

Leicester
Northampton
London

engineering excellence | creating advantage

Client:
St Helens Pharmacy Ltd

Architect:
Ascot Design

Project:
33 Prestbury Road
Wilmslow
SK9 2LJ

Title:
Superstructure
Main House
Connection Details

Status:

TENDER

Engineer:	JKT	Date:	September 2025
Drawn:	JD	Scales @ A1:	
Checked:	HP	1:10	
Project No:	64410	Drg No:	306
		Rev:	T2