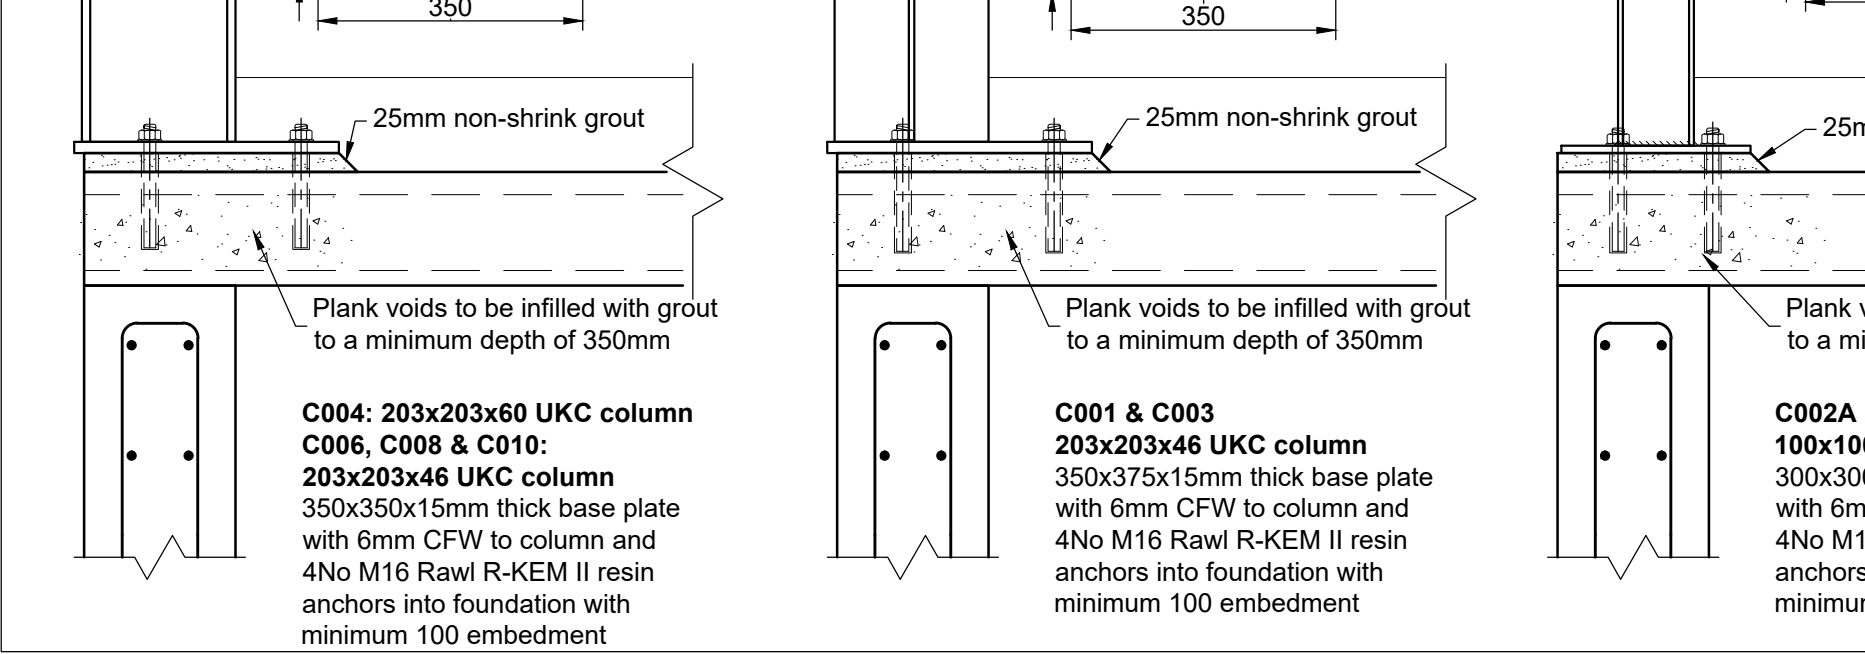
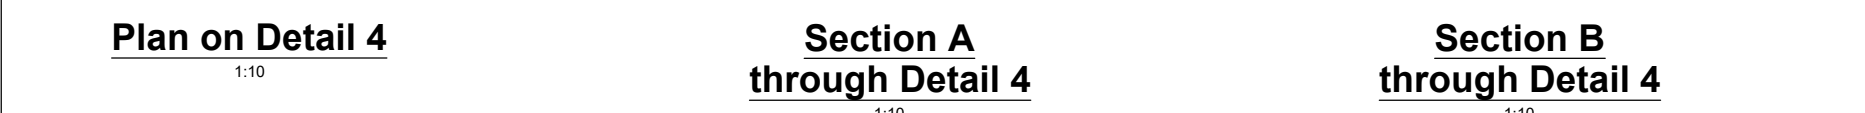


Notes:

1. PRP have assumed the role of a Designer in the context of the Construction (Design and Management) Regulations and The Building Safety Act. All parties must be aware of their duties under this legislation.
2. Construction work shall not be started until designs have been approved by Building Control.
3. Do not scale from this drawing.
4. All dimensions are in millimetres unless noted otherwise. All levels in metres unless noted otherwise.
5. Drawing shall be read in conjunction with all relevant architect's drawings. The architect shall retain overall responsibility for dimensional control. Any inconsistencies shall be reported to PRP.
6. All levels and dimensions shall be checked on site before any work commences. Setting out remains the responsibility of others.
7. Buildings shall be constructed in accordance with Approved Document A of the Building Regulations.
8. Fire protection shall be constructed in accordance with Approved Document B of the Building Regulations.
9. Temporary works shall be designed by others to BS 5975
9. Fire protective measures shall be designed by the Architect or contractor in accordance with Approved Document B of the Building Regulations.
10. Waterproofing shall be designed by others in accordance with Approved Document C of the Building Regulations.
11. For more information see PRP drawings:
 - 64410 - 100series - Drainage and External Works
 - 64410 - 200series - Foundations
 - 64410 - 300series - Superstructure
12. This drawing must be read together with PRP drawings:
 - 64410 - 300 - Typical Notes and Details

05x165x40 UKB 180 50 80 50 220x220x10mm thk flange plate with 6mm CFW to C008

le plate with
W to C008
B107:

160x220x10mm thk end plate with 6mm CFW to Tie 3 & 4 No M16 Grade 8.8 bolts to C008 flange plate

and plate with
7 & 4No M16
flange plate

Section B
through Detail 8

Client:

Architect:
Asset Design

Project:
33 Prestbury Road

Wilmslow
SK9 2LJ

Superstructure
Leisure Suite

Status: **TENDER**

Engineer:	CT	Date:	September 2025
Drawn:	JD	Scales @ A 1:	

Checked:	HP	1:10	
Project No:	64410	Drg No: 312	Rev: T2

© copyright all rights reserved. BPP UK Ltd

© copyright all rights reserved PRP.UK L