


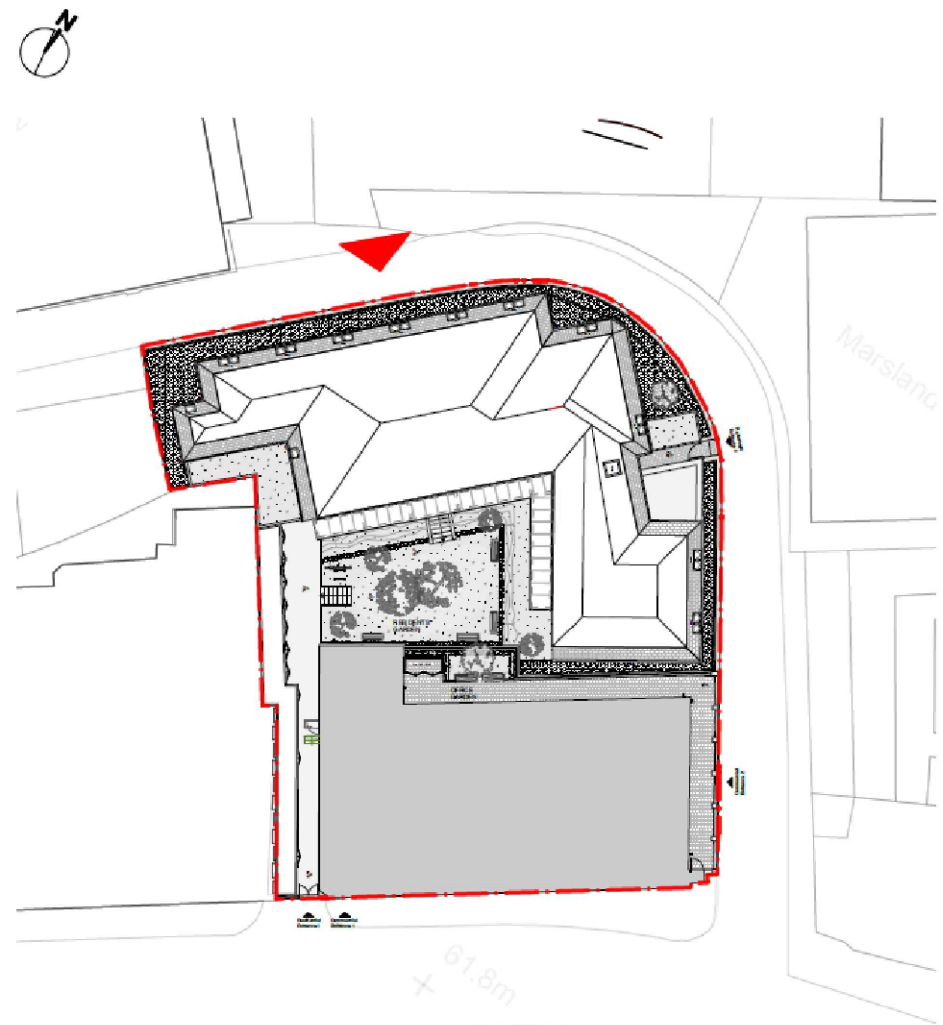

SEE EL05 FOR WALL TIE
NOTES AND DETAILS

LINTEL KEY:
LINTEL L1 - CATNIC CCS
LINTEL L2 - CATNIC ANG
LINTEL L3 - CATNIC SPECIAL ARCH LINTEL

NORTH ELEVATION
1:50 @ A1
1:100 @ A3

SEE J8897/EC01-EC03
FOR NOTES

PRELIMINARY

INITIAL ISSUE		12/11/25	CR
REV	COMMENTS	DATE	BY
BMC			
BELL MUNRO CONSULTING LTD			
CONSULTING CIVIL & STRUCTURAL ENGINEERS TURING HOUSE 5 ARCHWAY MANCHESTER M15 5RL TEL: 0161 2098032 FAX: 0161 2098033 EMAIL: CONSULTING@BELLMUNRO.CO.UK WWW.BELLMUNRO.CO.UK			
CLIENT: OLLIER SMURTHWAITE			
PROJECT: SEATON HOUSE			
TITLE: NORTH ELEVATION			
DRAWN BY: MP	CHECKED BY: AM	SCALE: AS SHOWN	DATE: 10/25
DRAWING NUMBER: J8897 EL01			REVISION: -