


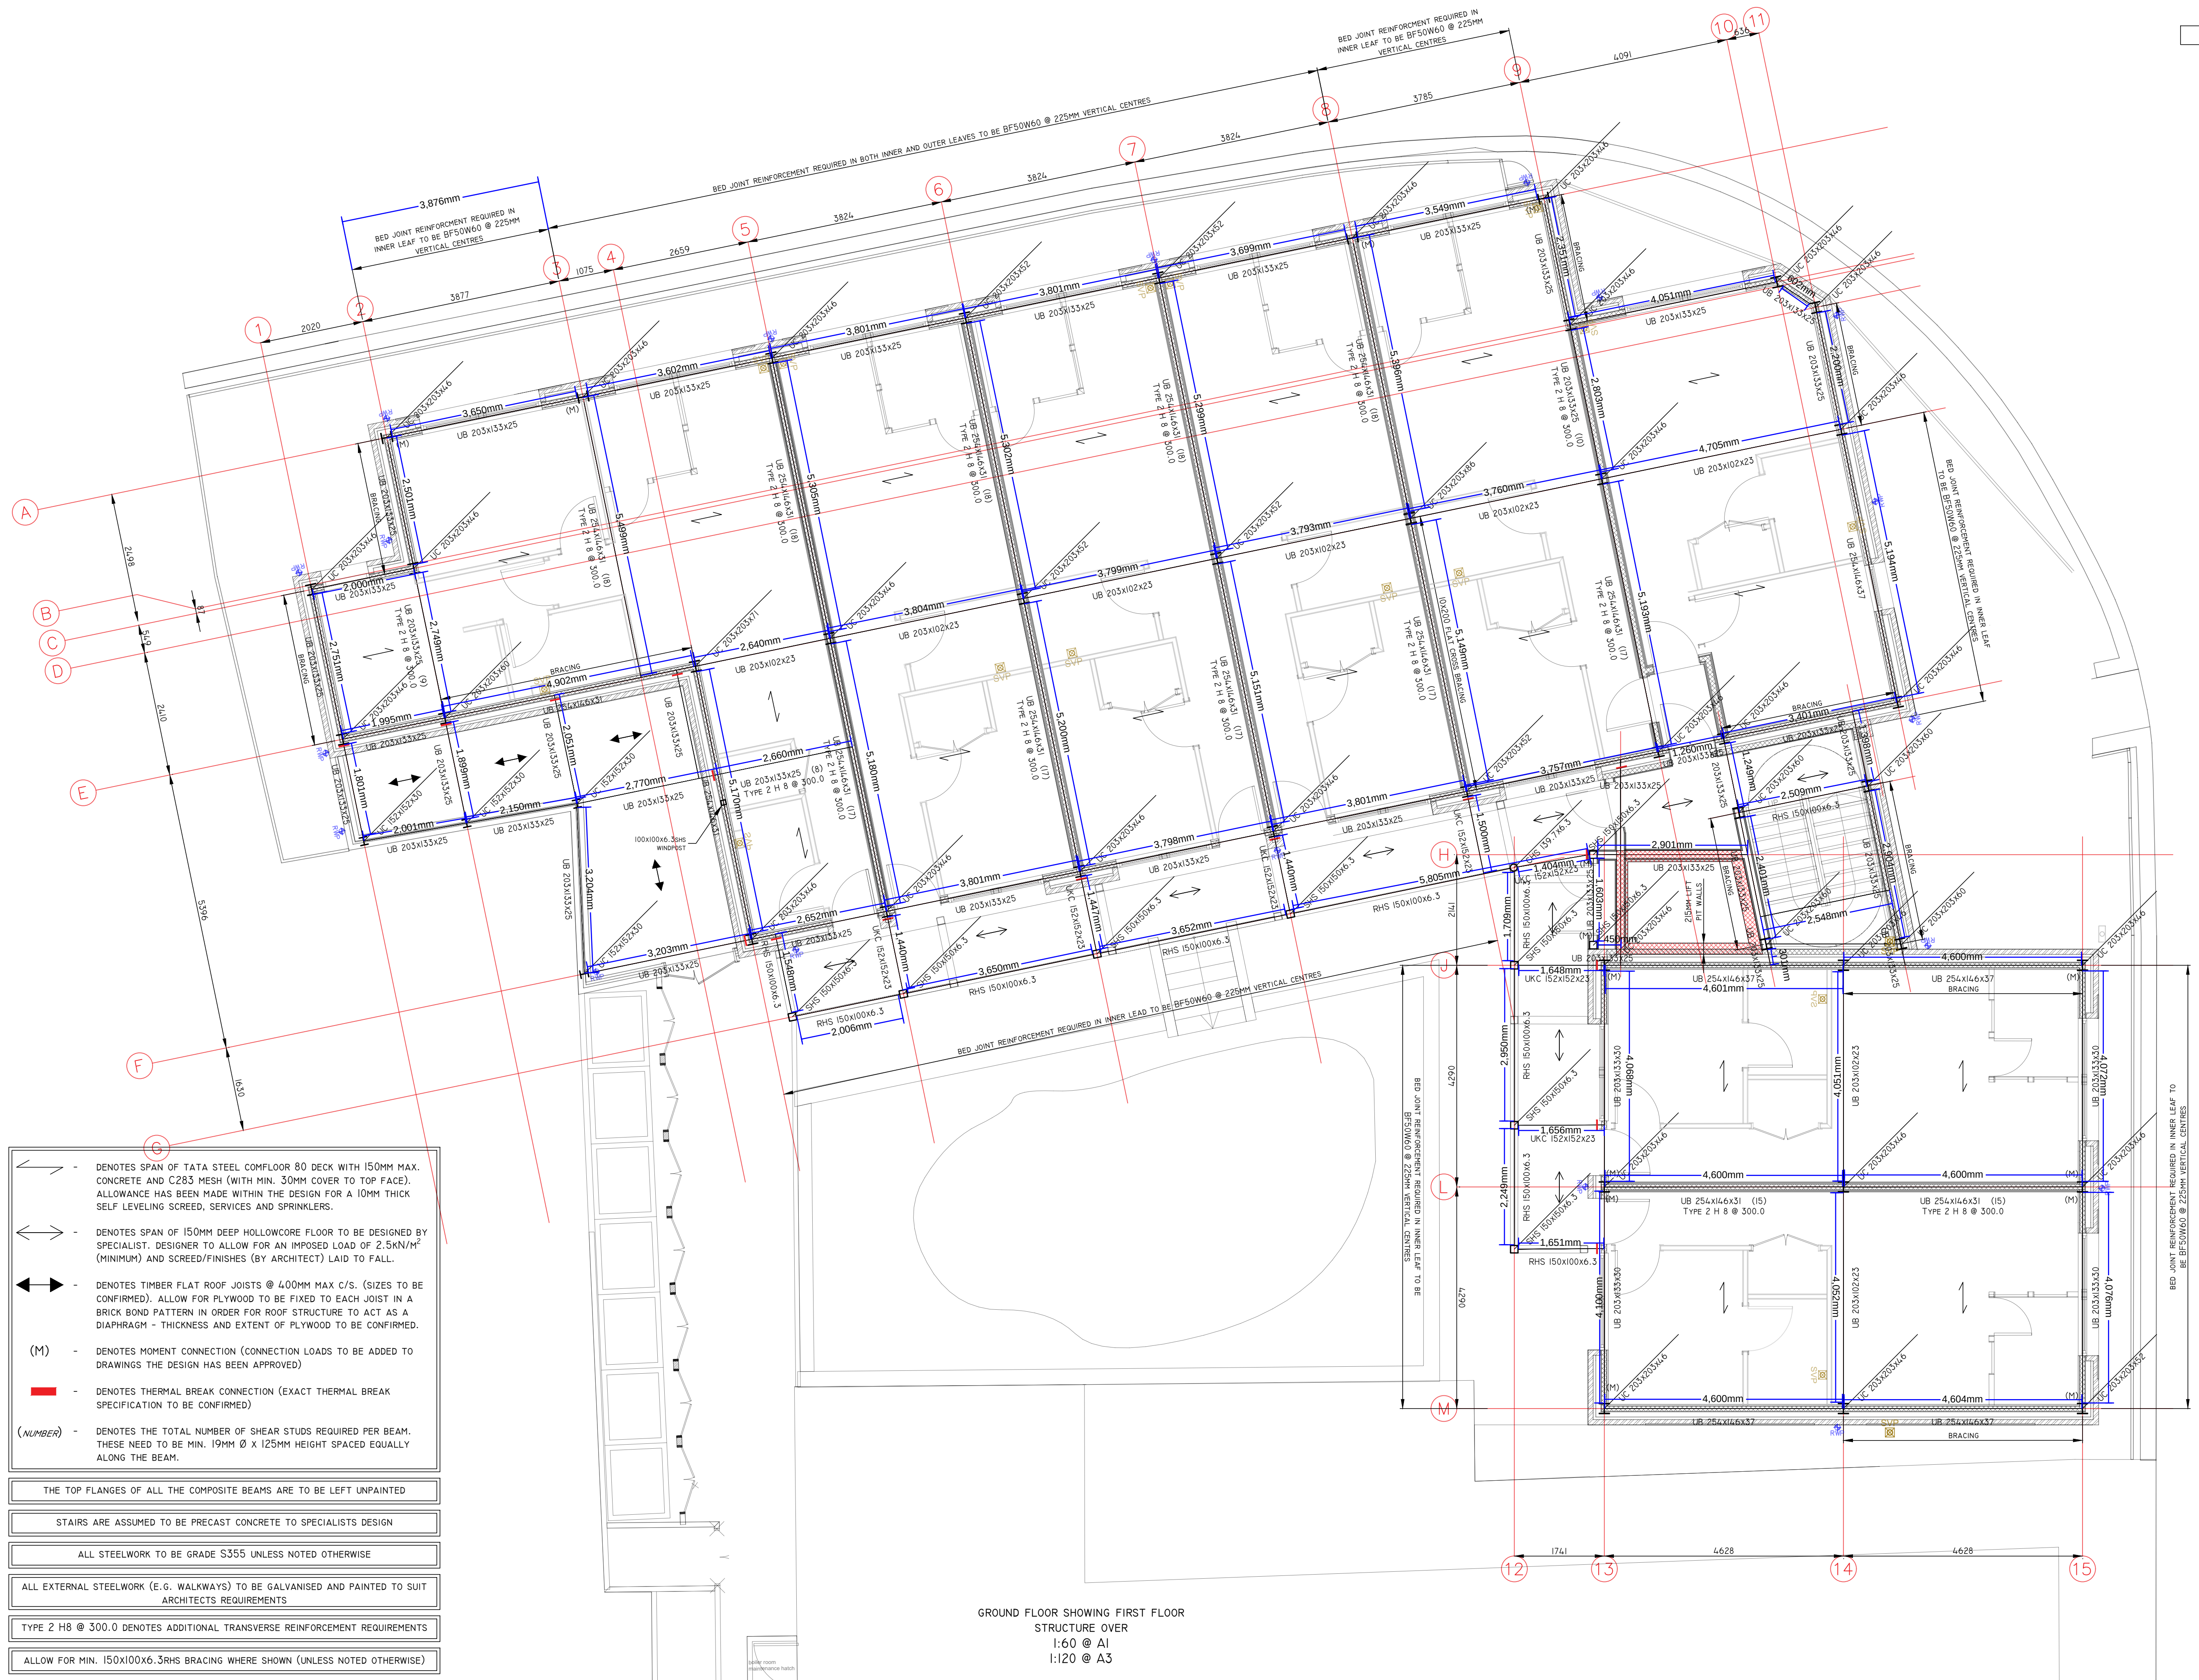

PRELIMINARY

C	SPS TO BLOCKWORK UPDATE	18/12/25	CR
B	AMENDS	10/11/25	CR
A	AMENDS	17/10/25	CR
-	INITIAL ISSUE	26/09/25	CR
REV	COMMENTS	DATE	BY

BMC

BELL MUNRO
CONSULTING LTD

CONSULTING CIVIL & STRUCTURAL ENGINEERS
TURNING HOUSE
5 ARCHWAY
MANCHESTER
M15 5RL
TEL: 0161 2098032 FAX: 0161 2098033
EMAIL: CONSULTING@BELLMUNRO.CO.UK
WWW.BELLMUNRO.CO.UK

CLIENT: OLLIER SMURTHWAITE

PROJECT: SEATON HOUSE

TITLE: GROUND FLOOR
SHOWING STRUCTURE OVER

DRAWN BY: CR CHECKED BY: AM SCALE: AS SHOWN DATE: 09/25

DRAWING NUMBER: J8897/S02 REVISION: C