


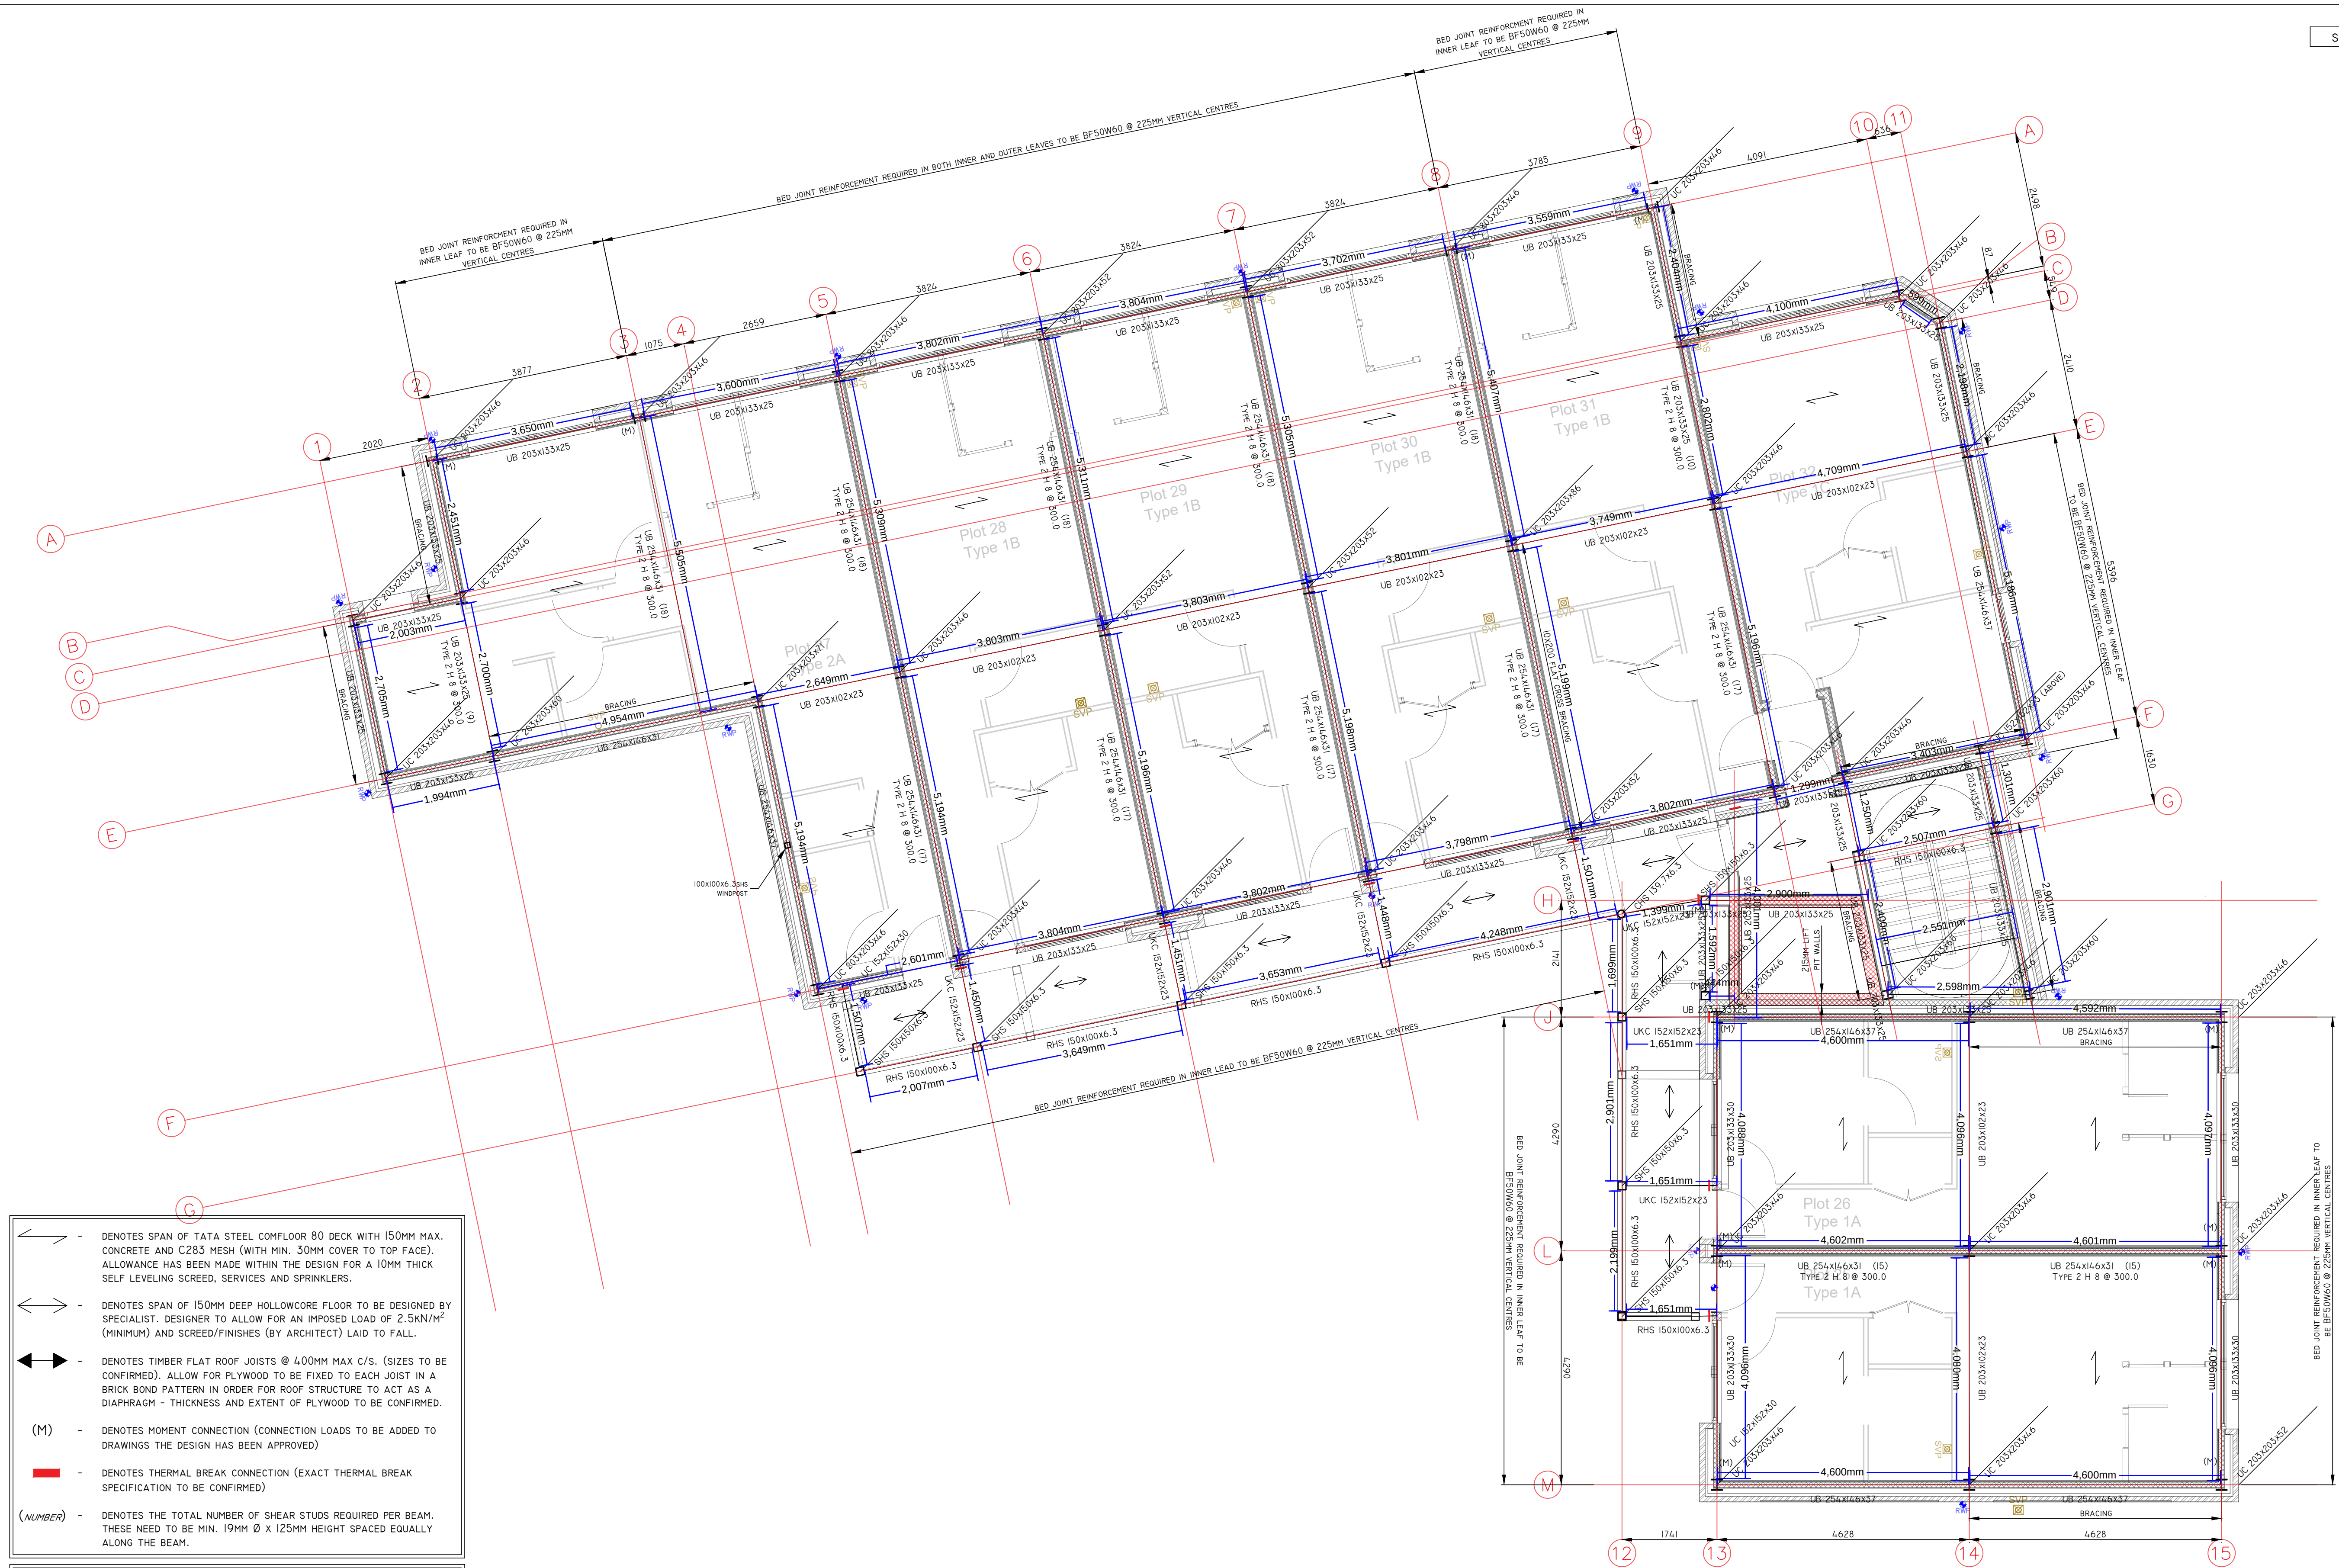

- ← - DENOTES SPAN OF TATA STEEL COMFLOOR 80 DECK WITH 150MM MAX. CONCRETE AND C283 MESH (WITH MIN. 30MM COVER TO TOP FACE). ALLOWANCE HAS BEEN MADE WITHIN THE DESIGN FOR A 10MM THICK SELF LEVELING SCREED, SERVICES AND SPRINKLERS.
- ↔ - DENOTES SPAN OF 150MM DEEP HOLLOWCORE FLOOR TO BE DESIGNED BY SPECIALIST. DESIGNER TO ALLOW FOR AN IMPOSED LOAD OF 2.5kN/M² (MINIMUM) AND SCREED/FINISHES (BY ARCHITECT) LAID TO FALL.
- ↔ - DENOTES TIMBER FLAT ROOF JOISTS @ 400MM MAX C/S. (SIZES TO BE CONFIRMED). ALLOW FOR PLYWOOD TO BE FIXED TO EACH JOIST IN A BRICK BOND PATTERN IN ORDER FOR ROOF STRUCTURE TO ACT AS A DIAPHRAGM - THICKNESS AND EXTENT OF PLYWOOD TO BE CONFIRMED.
- (M) - DENOTES MOMENT CONNECTION (CONNECTION LOADS TO BE ADDED TO DRAWINGS THE DESIGN HAS BEEN APPROVED)
- - DENOTES THERMAL BREAK CONNECTION (EXACT THERMAL BREAK SPECIFICATION TO BE CONFIRMED)
- (NUMBER) - DENOTES THE TOTAL NUMBER OF SHEAR STUDS REQUIRED PER BEAM. THESE NEED TO BE MIN. 19MM Ø X 125MM HEIGHT SPACED EQUALLY ALONG THE BEAM.

THE TOP FLANGES OF ALL THE COMPOSITE BEAMS ARE TO BE LEFT UNPAINTED

STAIRS ARE ASSUMED TO BE PRECAST CONCRETE TO SPECIALISTS DESIGN

ALL STEELWORK TO BE GRADE S355 UNLESS NOTED OTHERWISE

ALL EXTERNAL STEELWORK (E.G. WALKWAYS) TO BE GALVANISED AND PAINTED TO SUIT ARCHITECTS REQUIREMENTS

TYPE 2 H8 @ 300.0 DENOTES ADDITIONAL TRANSVERSE REINFORCEMENT REQUIREMENTS

ALLOW FOR MIN. 150x100x6.3RHS BRACING WHERE SHOWN (UNLESS NOTED OTHERWISE)

SECOND FLOOR SHOWING THIRD FLOOR
STRUCTURE OVER
1:50 @ A1
1:100 @ A3

PRELIMINARY

C	SFS TO BLOCKWORK UPDATE	18/12/25	CR
B	AMENDS	10/11/25	CR
A	AMENDS	17/10/25	CR
-	INITIAL ISSUE	26/09/25	CR
REV	COMMENTS	DATE	BY

BMC

BELL MUNRO
CONSULTING LTD

CONSULTING CIVIL & STRUCTURAL ENGINEERS
TURNING HOUSE
5 ARCHWAY
MANCHESTER
M15 5RL
TEL: 0161 2098032
FAX: 0161 2098033
EMAIL: CONSULTING@BELLMUNRO.CO.UK
WWW.BELLMUNRO.CO.UK

CLIENT: OLLIER SMURTHWAITE

PROJECT: SEATON HOUSE

TITLE: SECOND FLOOR
SHOWING STRUCTURE OVER

DRAWN BY: CR
CHECKED BY: AM
SCALE: AS SHOWN
DATE: 09/25

DRAWING NUMBER: J8897/S04
REVISION: C