




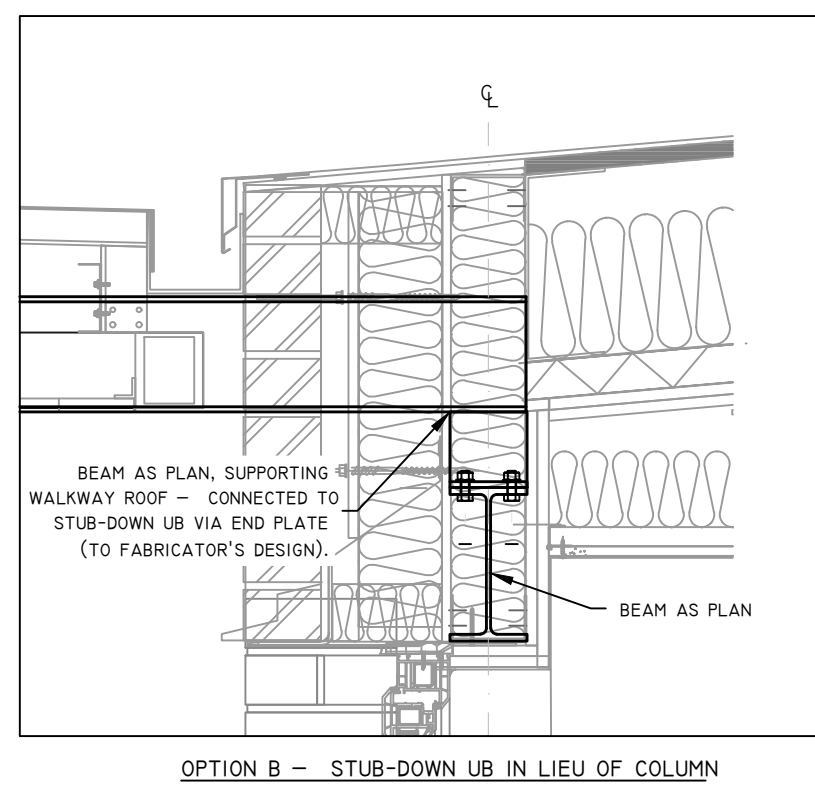


SETTING OUT OF STEELWORK, WALL WIDTHS, CAVITY POSITIONS AND CONSTRUCTION BUILD-UPS TO BE CONFIRMED AND DETAILED BY ARCHITECT. STRUCTURAL ELEMENTS SHOWN FOR COORDINATION ONLY. ALL FAÇADE FIXINGS, INSULATION INTERFACES AND FIRE-STOPPING TO BE COORDINATED WITH ARCHITECTURAL AND FIRE DESIGN REQUIREMENTS.

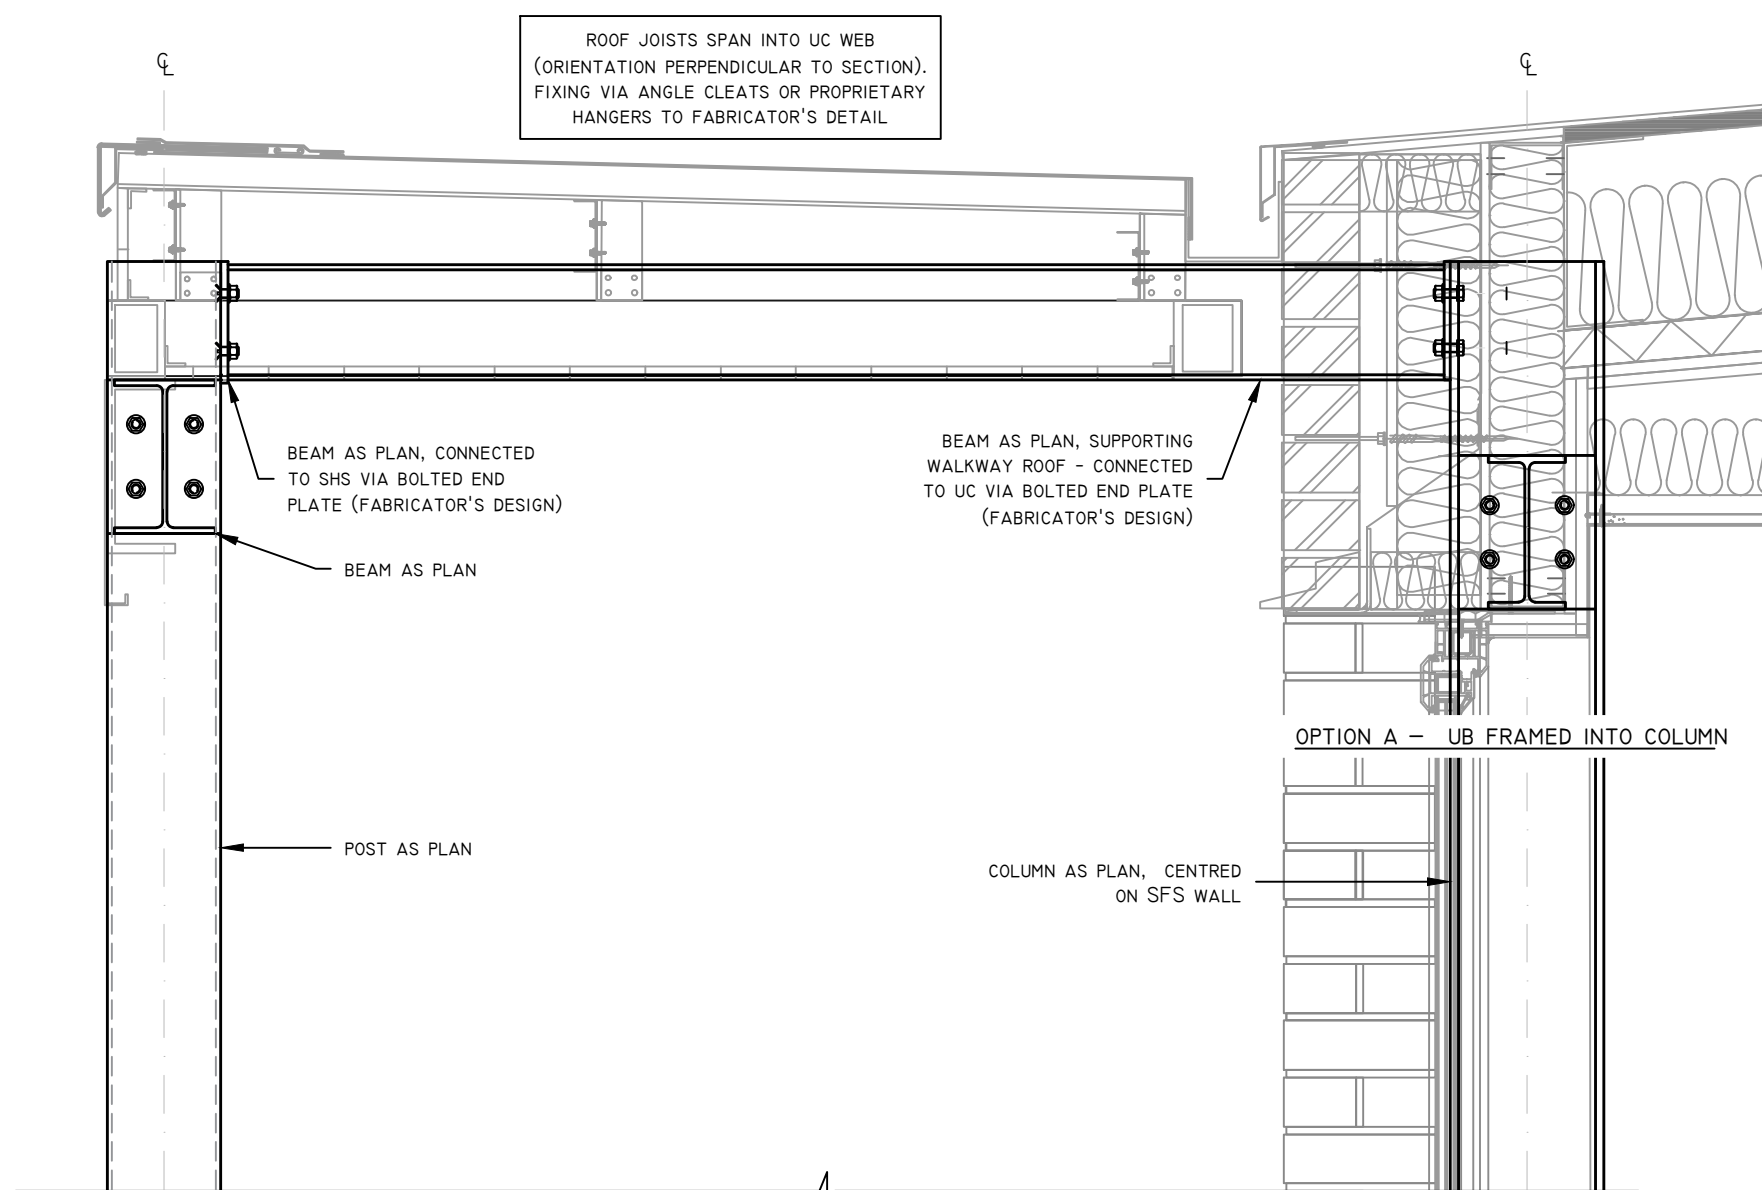


ALL STEEL CONNECTIONS TO FABRICATOR'S DESIGN AND APPROVAL. MEMBER SIZES AND LOCATIONS TO STRUCTURAL ENGINEER'S DESIGN.

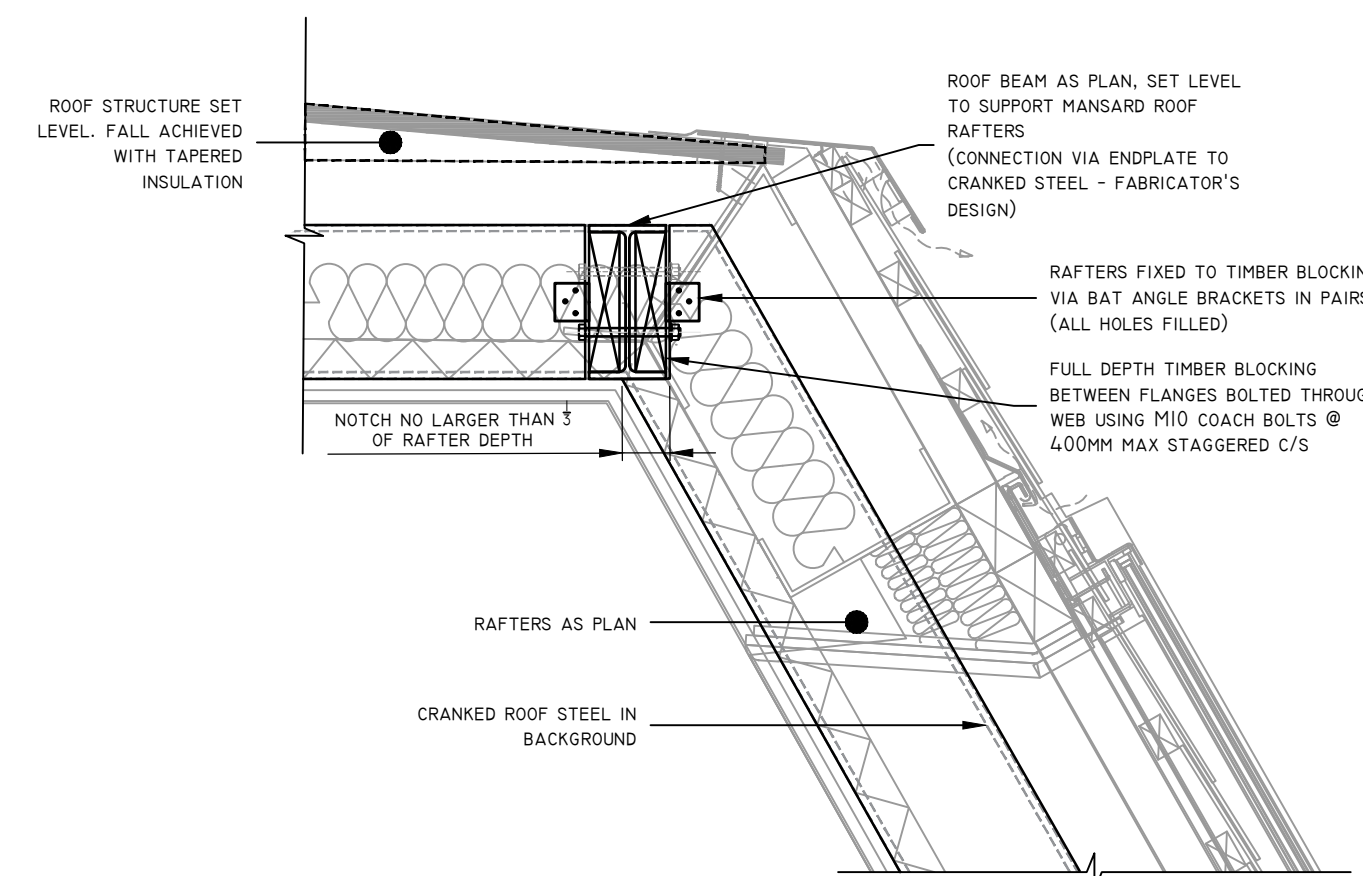

MANSARD ROOF / FLAT ROOF TRANSITION DETAIL
ARCHITECT DETAIL REF: A817-T-2012A
1:10 @ A1
1:20 @ A3

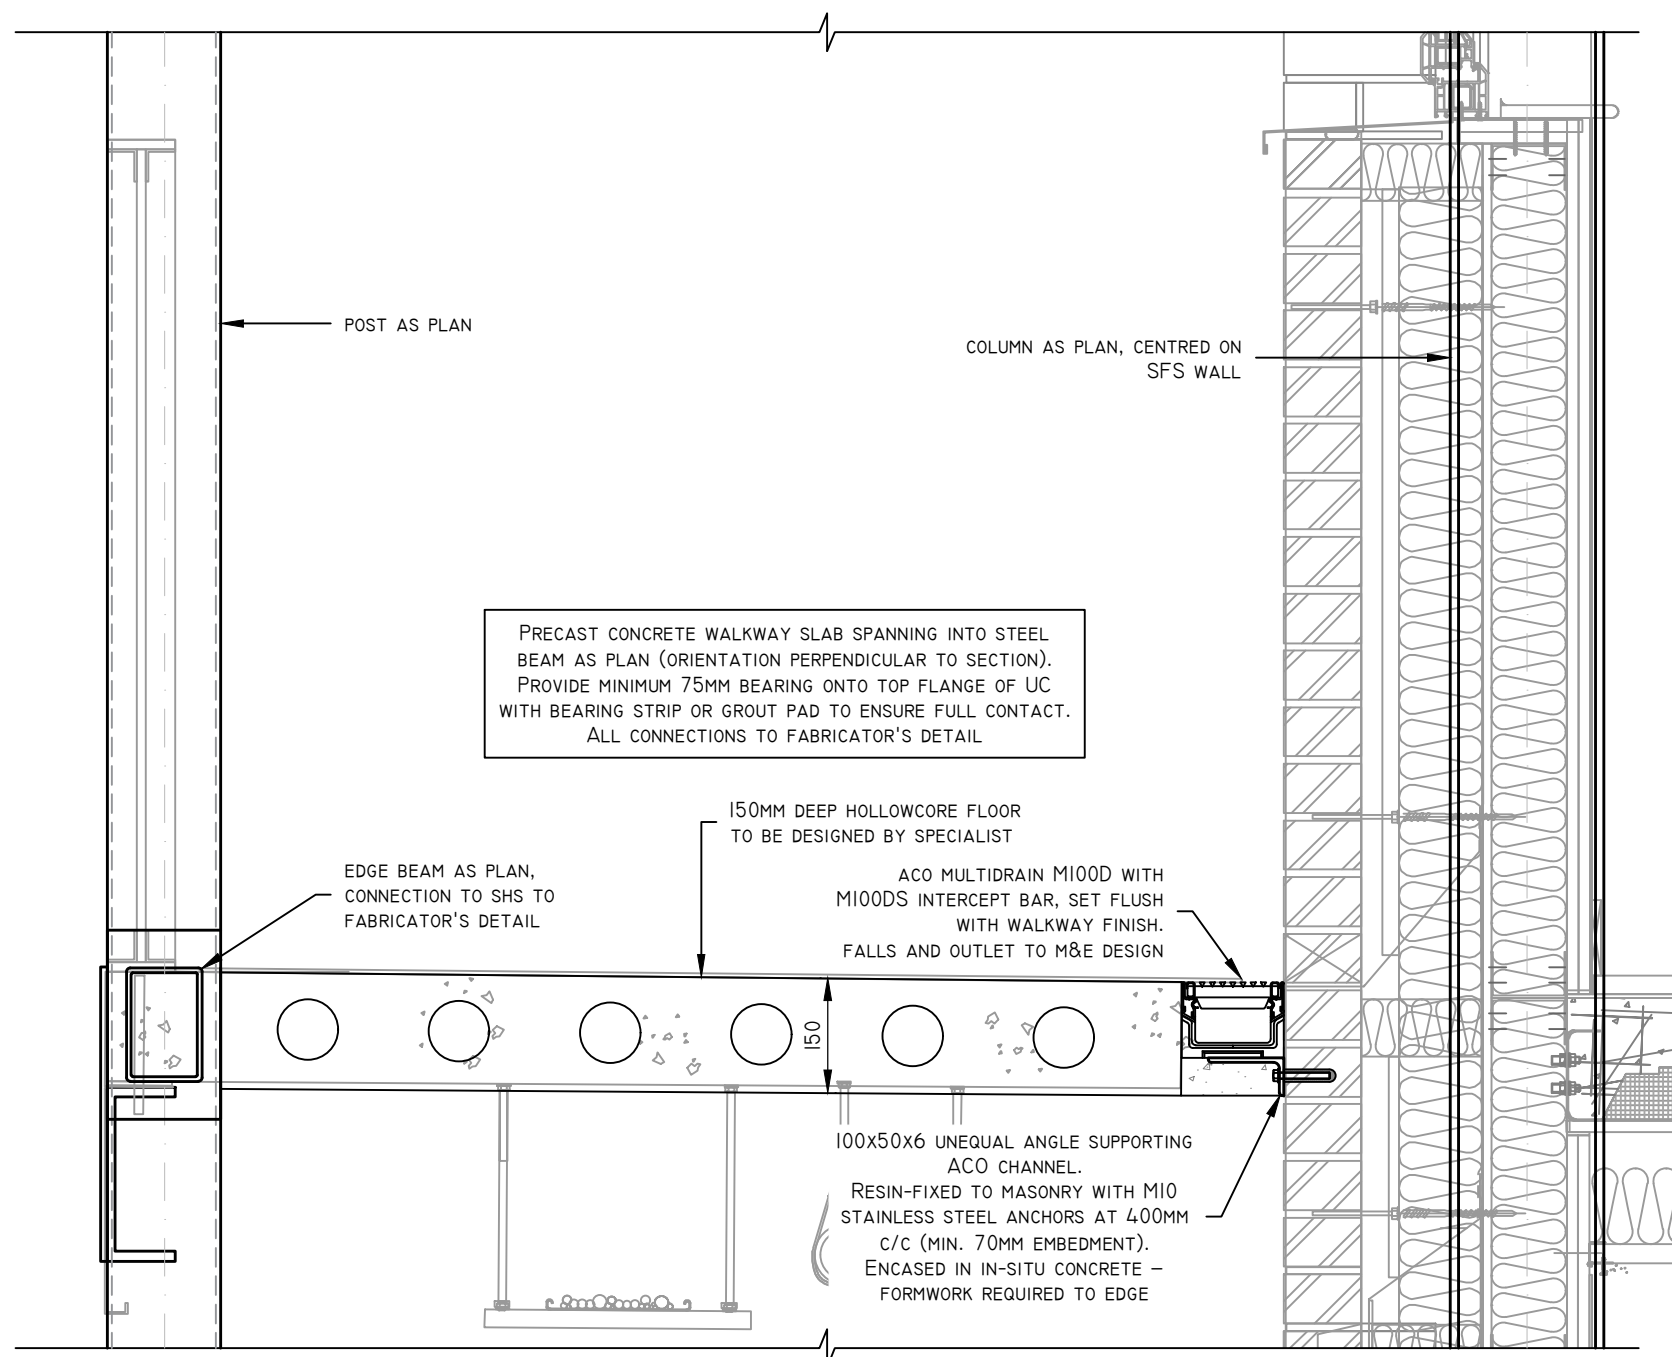


WALKWAY / ROOF INTERFACE DETAIL - COLUMN OR STUB CONNECTION OPTION
ARCHITECT DETAIL REF: A817-T-2014A
1:10 @ A1
1:20 @ A3

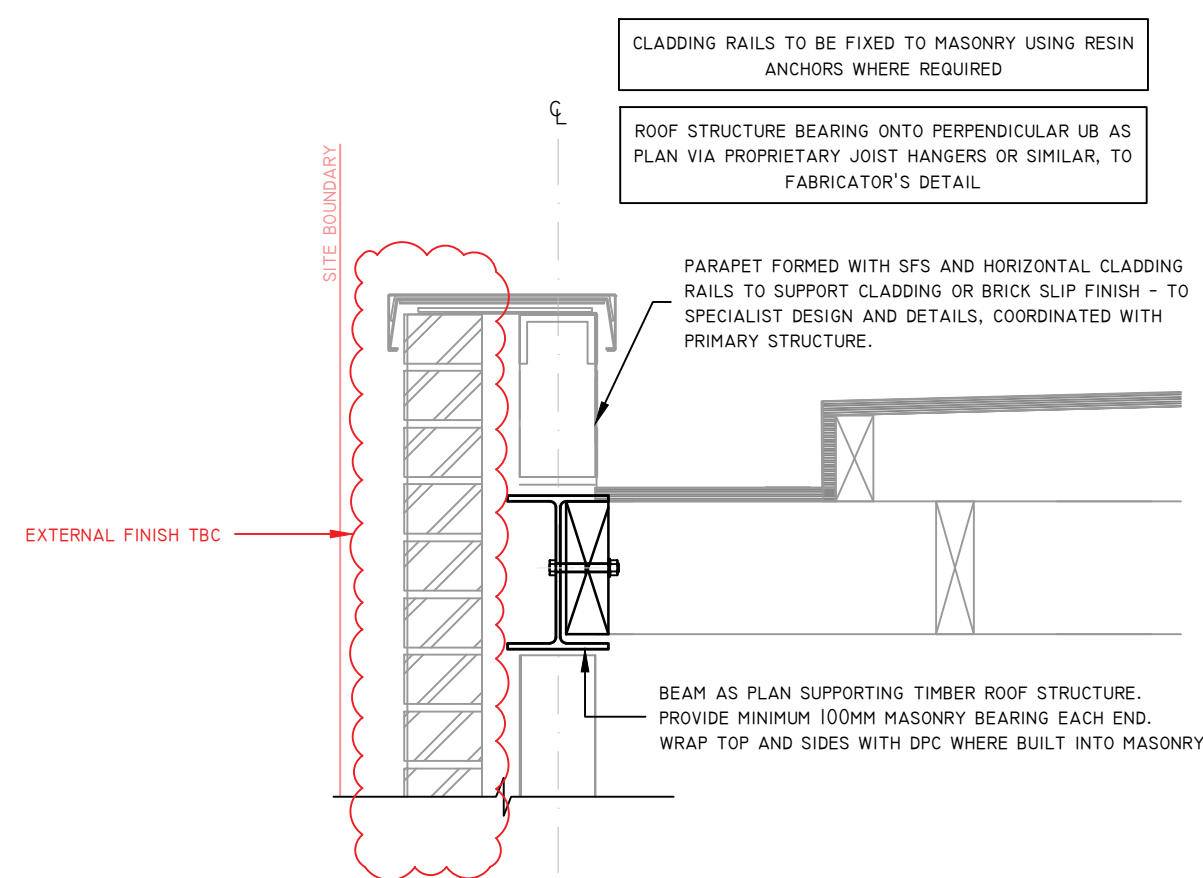


PLANT ROOF PARAPET DETAIL
ARCHITECT DETAIL REF: A817-T-2020B
1:10 @ A1
1:20 @ A3


ANCON OPTIMA/P SUPPORT SYSTEM - DENOTES USE OF ANCON MASONRY SUPPORT BRACKETS FIXED BACK TO PRIMARY STEEL VIA ANCON STEELGRIP TOGETHER WITH ISOLATION MATERIAL TO PREVENT BI-METALLIC CORROSION.
NOTE: NO-FIX ZONES AROUND COLUMN POSITIONS

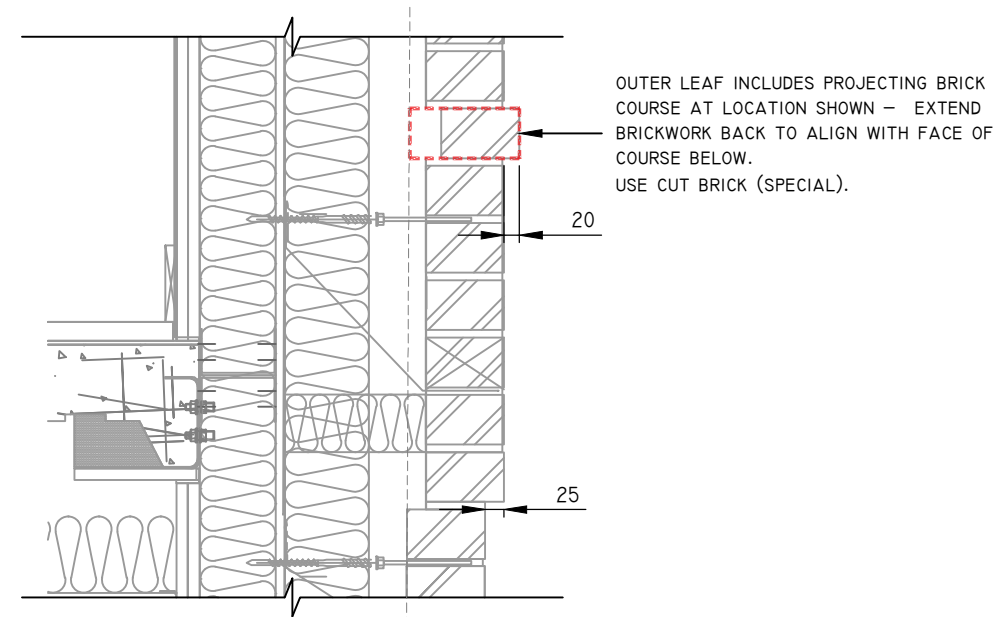


PROJECTING BRICK COURSE DETAIL
ARCHITECT DETAIL REF: A817-T-2010A
1:10 @ A1
1:20 @ A3

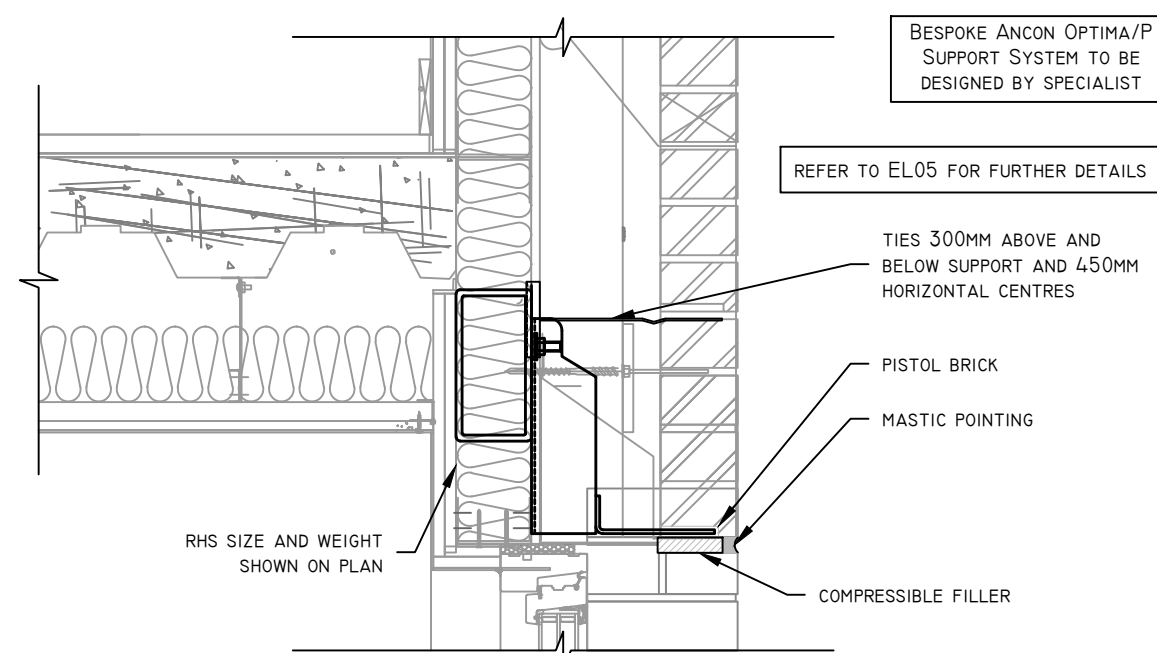

MASONRY SUPPORT ANGLE DETAIL
ARCHITECT DETAIL REF: A817-T-2004A
1:10 @ A1
1:20 @ A3

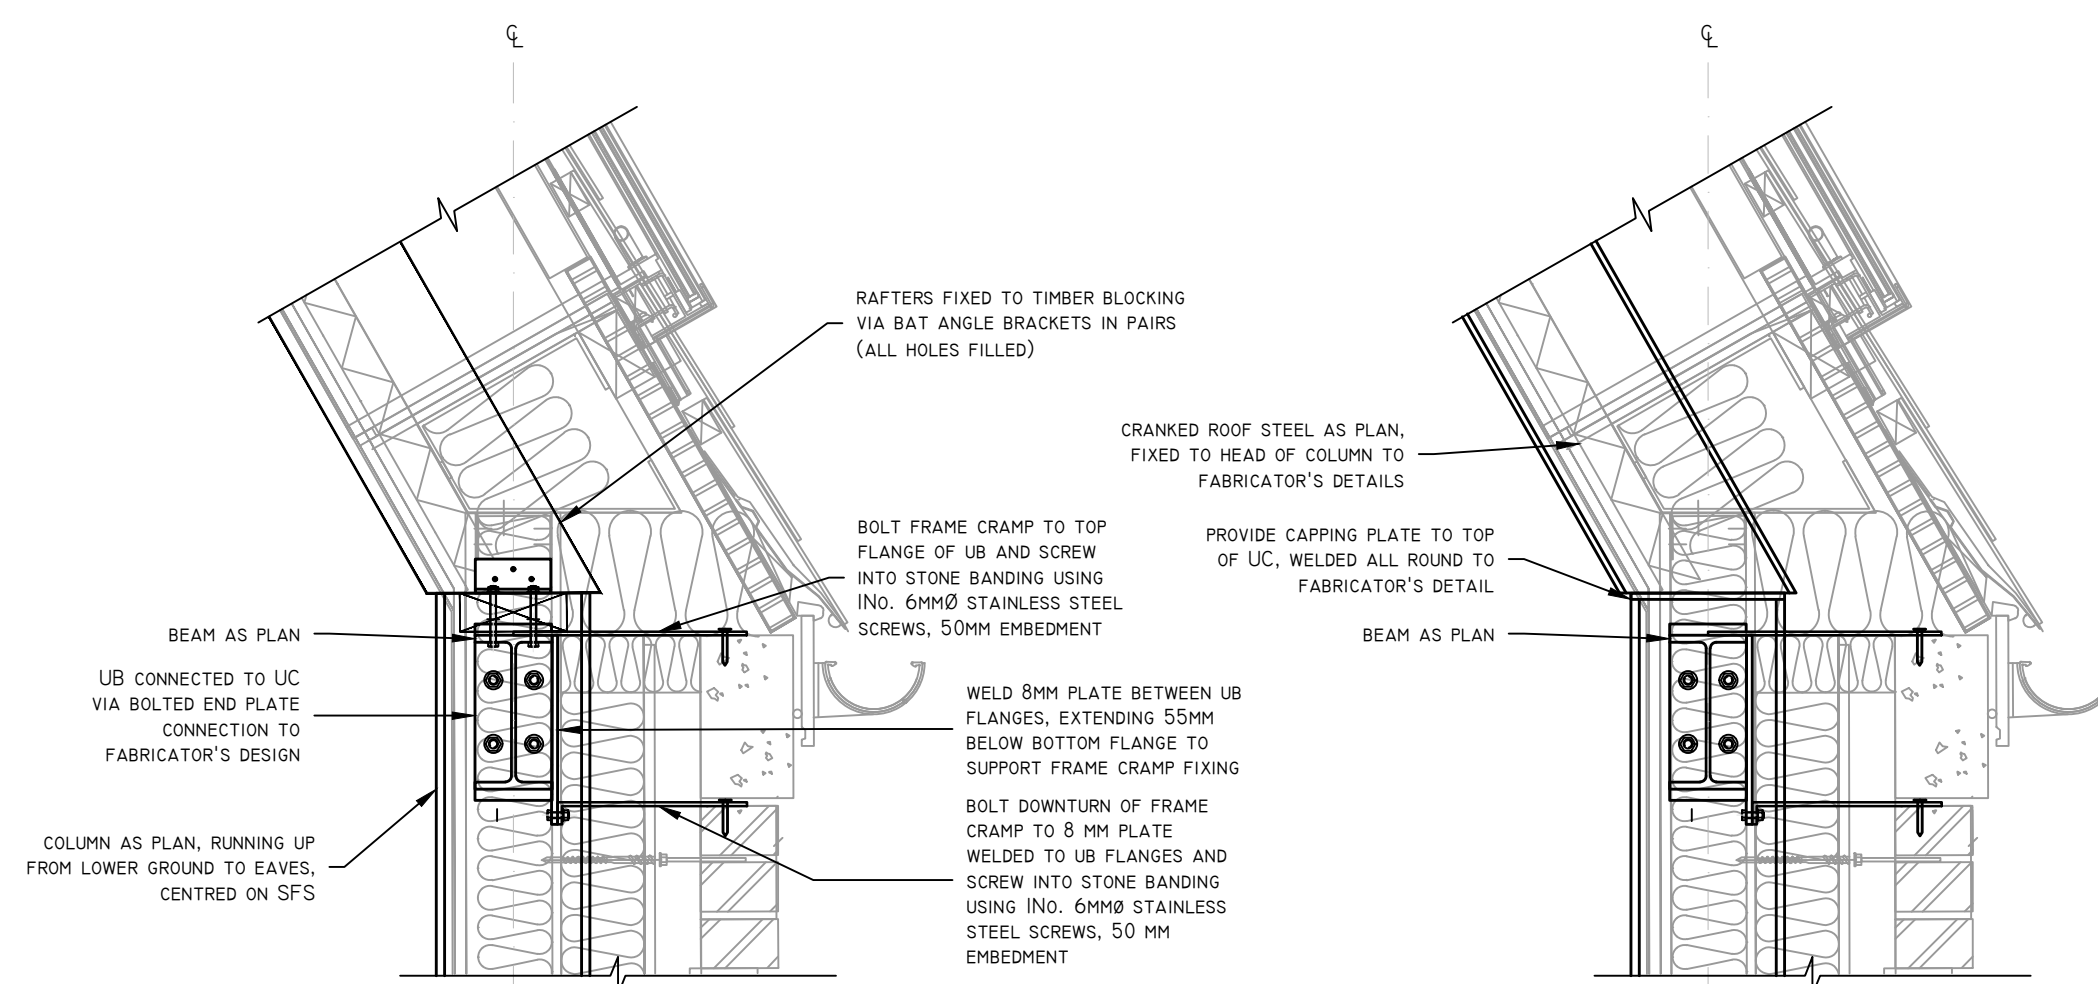

TOP OF WALL / EAVES DETAIL SHOWING RAFTER TO WALL PLATE AND CRANKED STEEL TO COLUMN
ARCHITECT DETAIL REF: A817-T-2011B
1:10 @ A1
1:20 @ A3

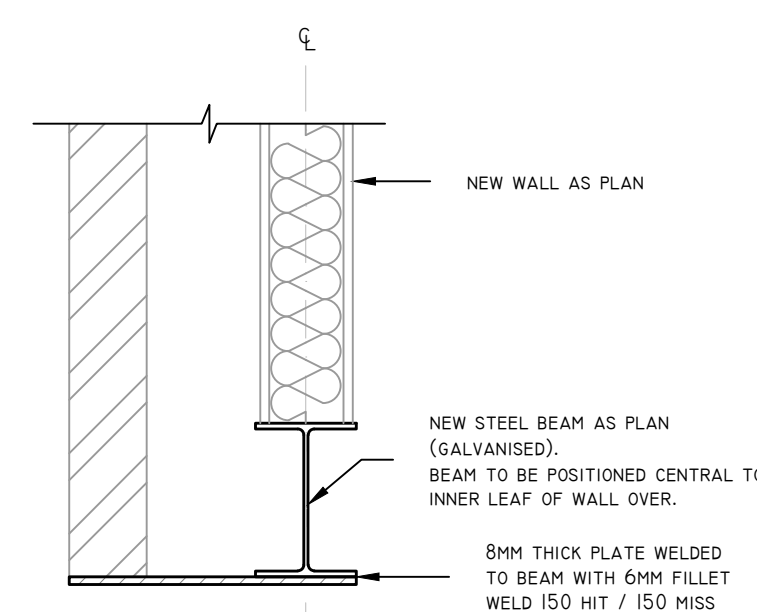

MASONRY SUPPORT DETAIL
1:10 @ A1
1:20 @ A3

PRELIMINARY

INITIAL ISSUE	12/11/25	
COMMENTS	DATE	

BMCBELL MUNRO
CONSULTING LTD

CONSULTING CIVIL & STRUCTURAL ENGINEERS
TURNING HOUSE
5 ARCHWAY
MANCHESTER
M15 5RL
TEL: 0161 2098032
FAX: 0161 2098033
EMAIL: CONSULTING@BELLMUNRO.CO.UK
WWW.BELLMUNRO.CO.UK

CLIENT: OLLIER SMURTHWAITE

PROJECT: SEATON HOUSE

TITLE: DETAILS

DRAWN BY: MP	CHECKED BY: AM	SCALE: AS SHOWN	DATE: 10/25
--------------	----------------	-----------------	-------------

DRAWING NUMBER: J8897 S06	REVISION: -
---------------------------	-------------